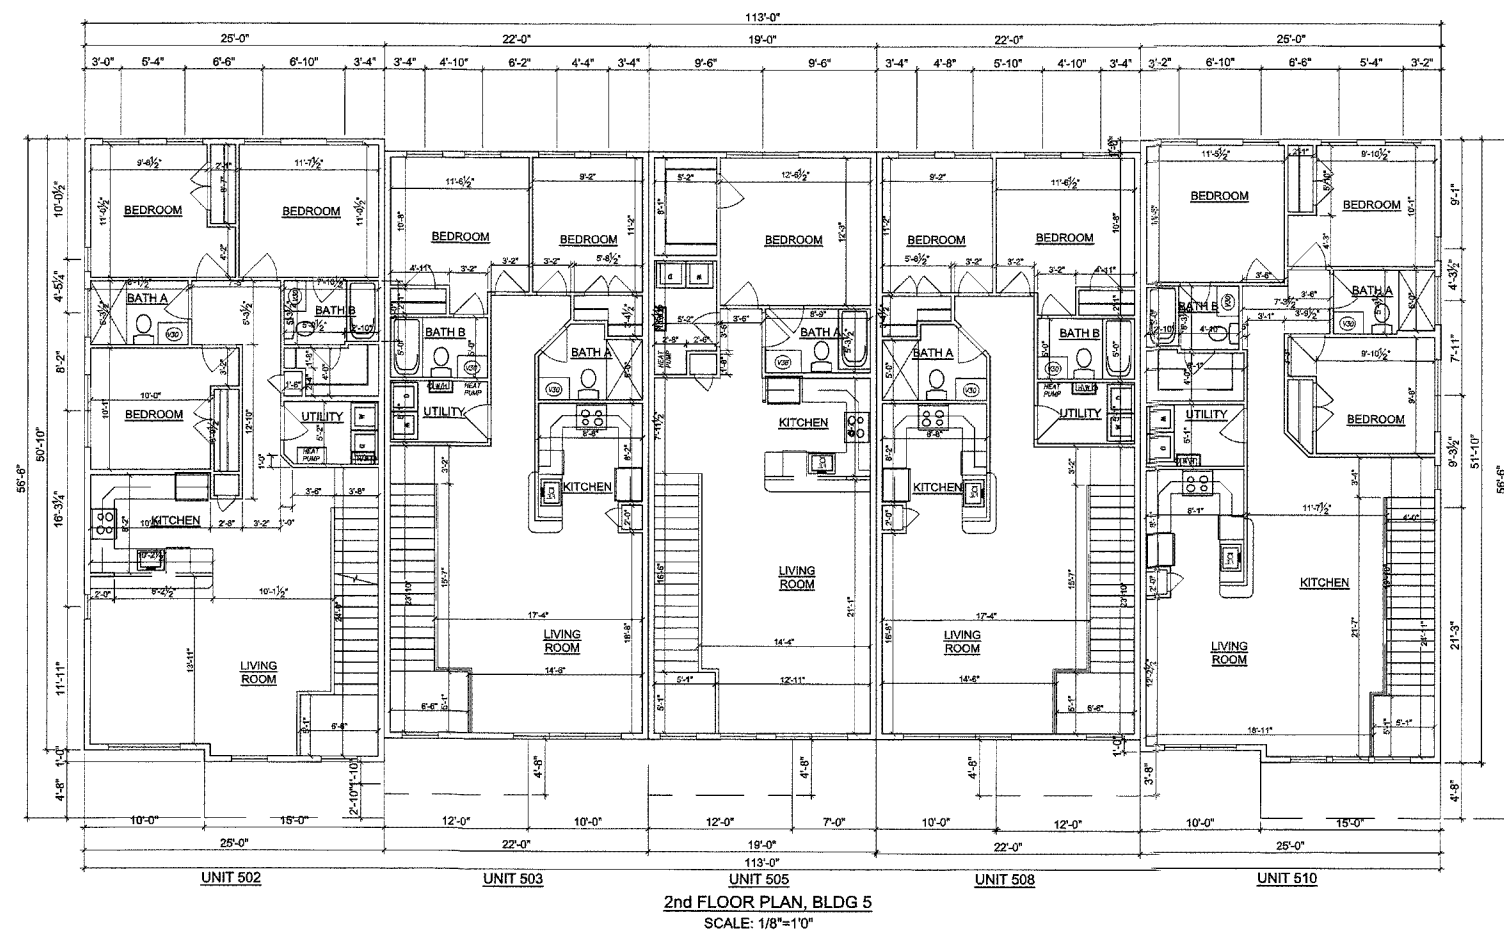
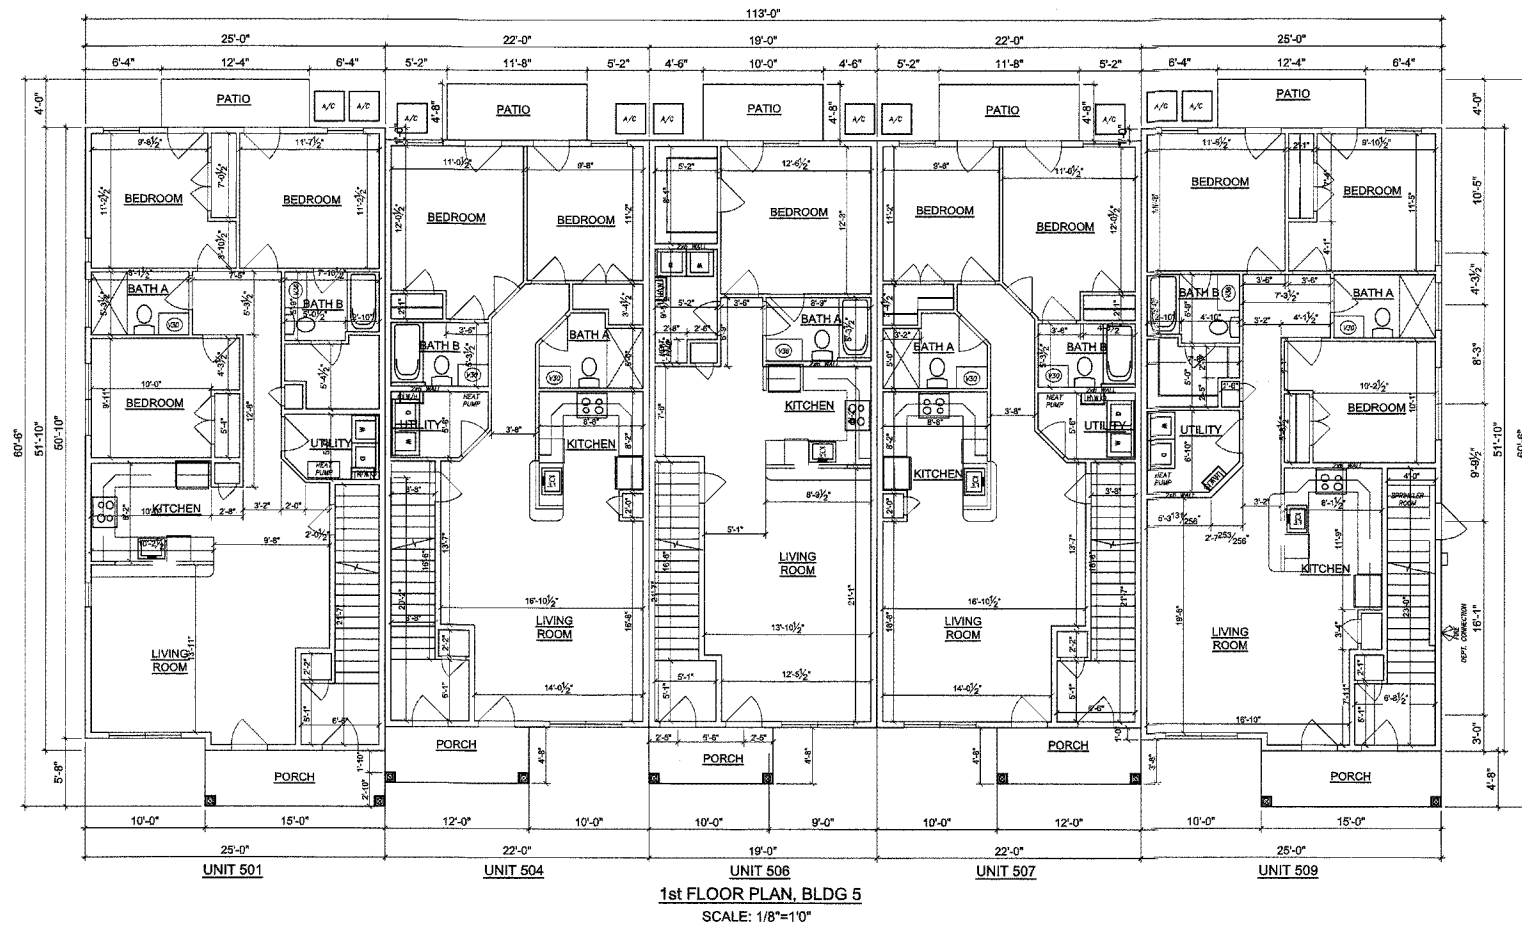







**DAVIS
BOWEN &
FRIEDEL, INC.**
ARCHITECTS • ENGINEERS • SURVEYORS
MILFORD, DELAWARE 19967
302.424.1441

**CONDOMINIUM DECLARATION PLAN
BUILDING 5
DUTCHMAN'S HARVEST
LEWES & REHOBOTH HUNDRED
CITY OF LEWES, SUSSEX COUNTY, DELAWARE**


DATE	COMMENTS

Date: AUGUST 13, 2026
Scale: AS SHOWN
Dwn.By: EHC
Proj.No.: 0818R001.K02

FLOOR PLANS

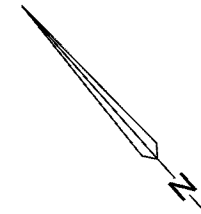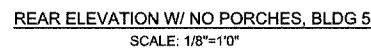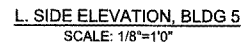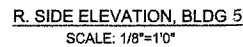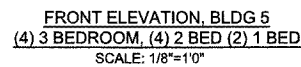

BUILDING 5 LOCATION		
LINE	BEARING	DISTANCE
1	S 46°31' 39" E	720.34
2	S 48°24' 39" E	6.42
3	N 4°12' 59" E	3.99
4	S 48°16' 59" E	3.91
5	S 41°35' 21" W	9.77
6	S 48°24' 39" E	6.24
7	S 41°35' 21" W	1.10
8	S 48°24' 39" E	9.75
9	N 41°35' 21" E	3.91
10	S 48°02' 45" E	11.62
11	S 41°35' 21" W	3.84
12	S 48°24' 39" E	9.75
13	N 41°35' 21" E	3.91
14	S 48°43' 07" E	9.99
15	S 41°35' 21" W	3.84
16	S 48°24' 39" E	9.75
17	N 41°35' 21" E	3.91
18	S 47°26' 55" E	11.59
19	S 41°35' 21" W	3.78
20	S 48°24' 39" E	5.12
21	N 41°35' 21" E	3.91
22	S 47°24' 39" E	6.25
23	N 41°35' 21" E	3.94
24	S 48°47' 36" E	12.53
25	S 41°35' 21" W	4.03
26	S 48°24' 39" E	9.75
27	S 41°38' 16" W	56.70
28	N 48°21' 44" W	15.00
29	N 41°38' 16" E	5.64
30	N 48°21' 44" W	10.03
31	S 41°38' 16" E	5.64
32	N 48°21' 44" W	12.07
33	N 41°38' 16" E	4.32
34	N 48°21' 44" W	18.65
35	S 41°38' 16" E	4.32
36	N 48°21' 44" W	10.31
37	N 41°38' 16" E	4.32
38	N 48°21' 44" W	10.17
39	S 41°38' 16" W	4.30
40	N 48°21' 44" W	10.37
41	S 41°38' 16" W	2.48
42	N 48°21' 44" W	15.20
43	N 41°38' 16" E	5.58
44	N 48°21' 44" W	10.31
45	N 41°38' 16" E	51.16

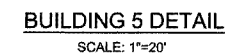

**DAVIS
BOWEN &
FRIEDEL, INC.**

ARCHITECTS • ENGINEERS • SURVEYORS

EASTON, MARYLAND MILFORD, DELAWARE SALISBURY, MARYLAND

**CONDOMINIUM DECLARATION PLAN
BUILDING 5
DUTCHMAN'S HARVEST
LEWES & REHOBOTH HUNDRED
CITY OF LEWES, SUSSEX COUNTY, DELAWARE**

[illegible]

Date:	AUGUST 13, 2026
Scale:	AS SHOWN
Dwn.By:	EHC
Proj.No.:	0818R001.K02

ELEVATIONS & DETAIL

Dwg.No.:
3 of 3