

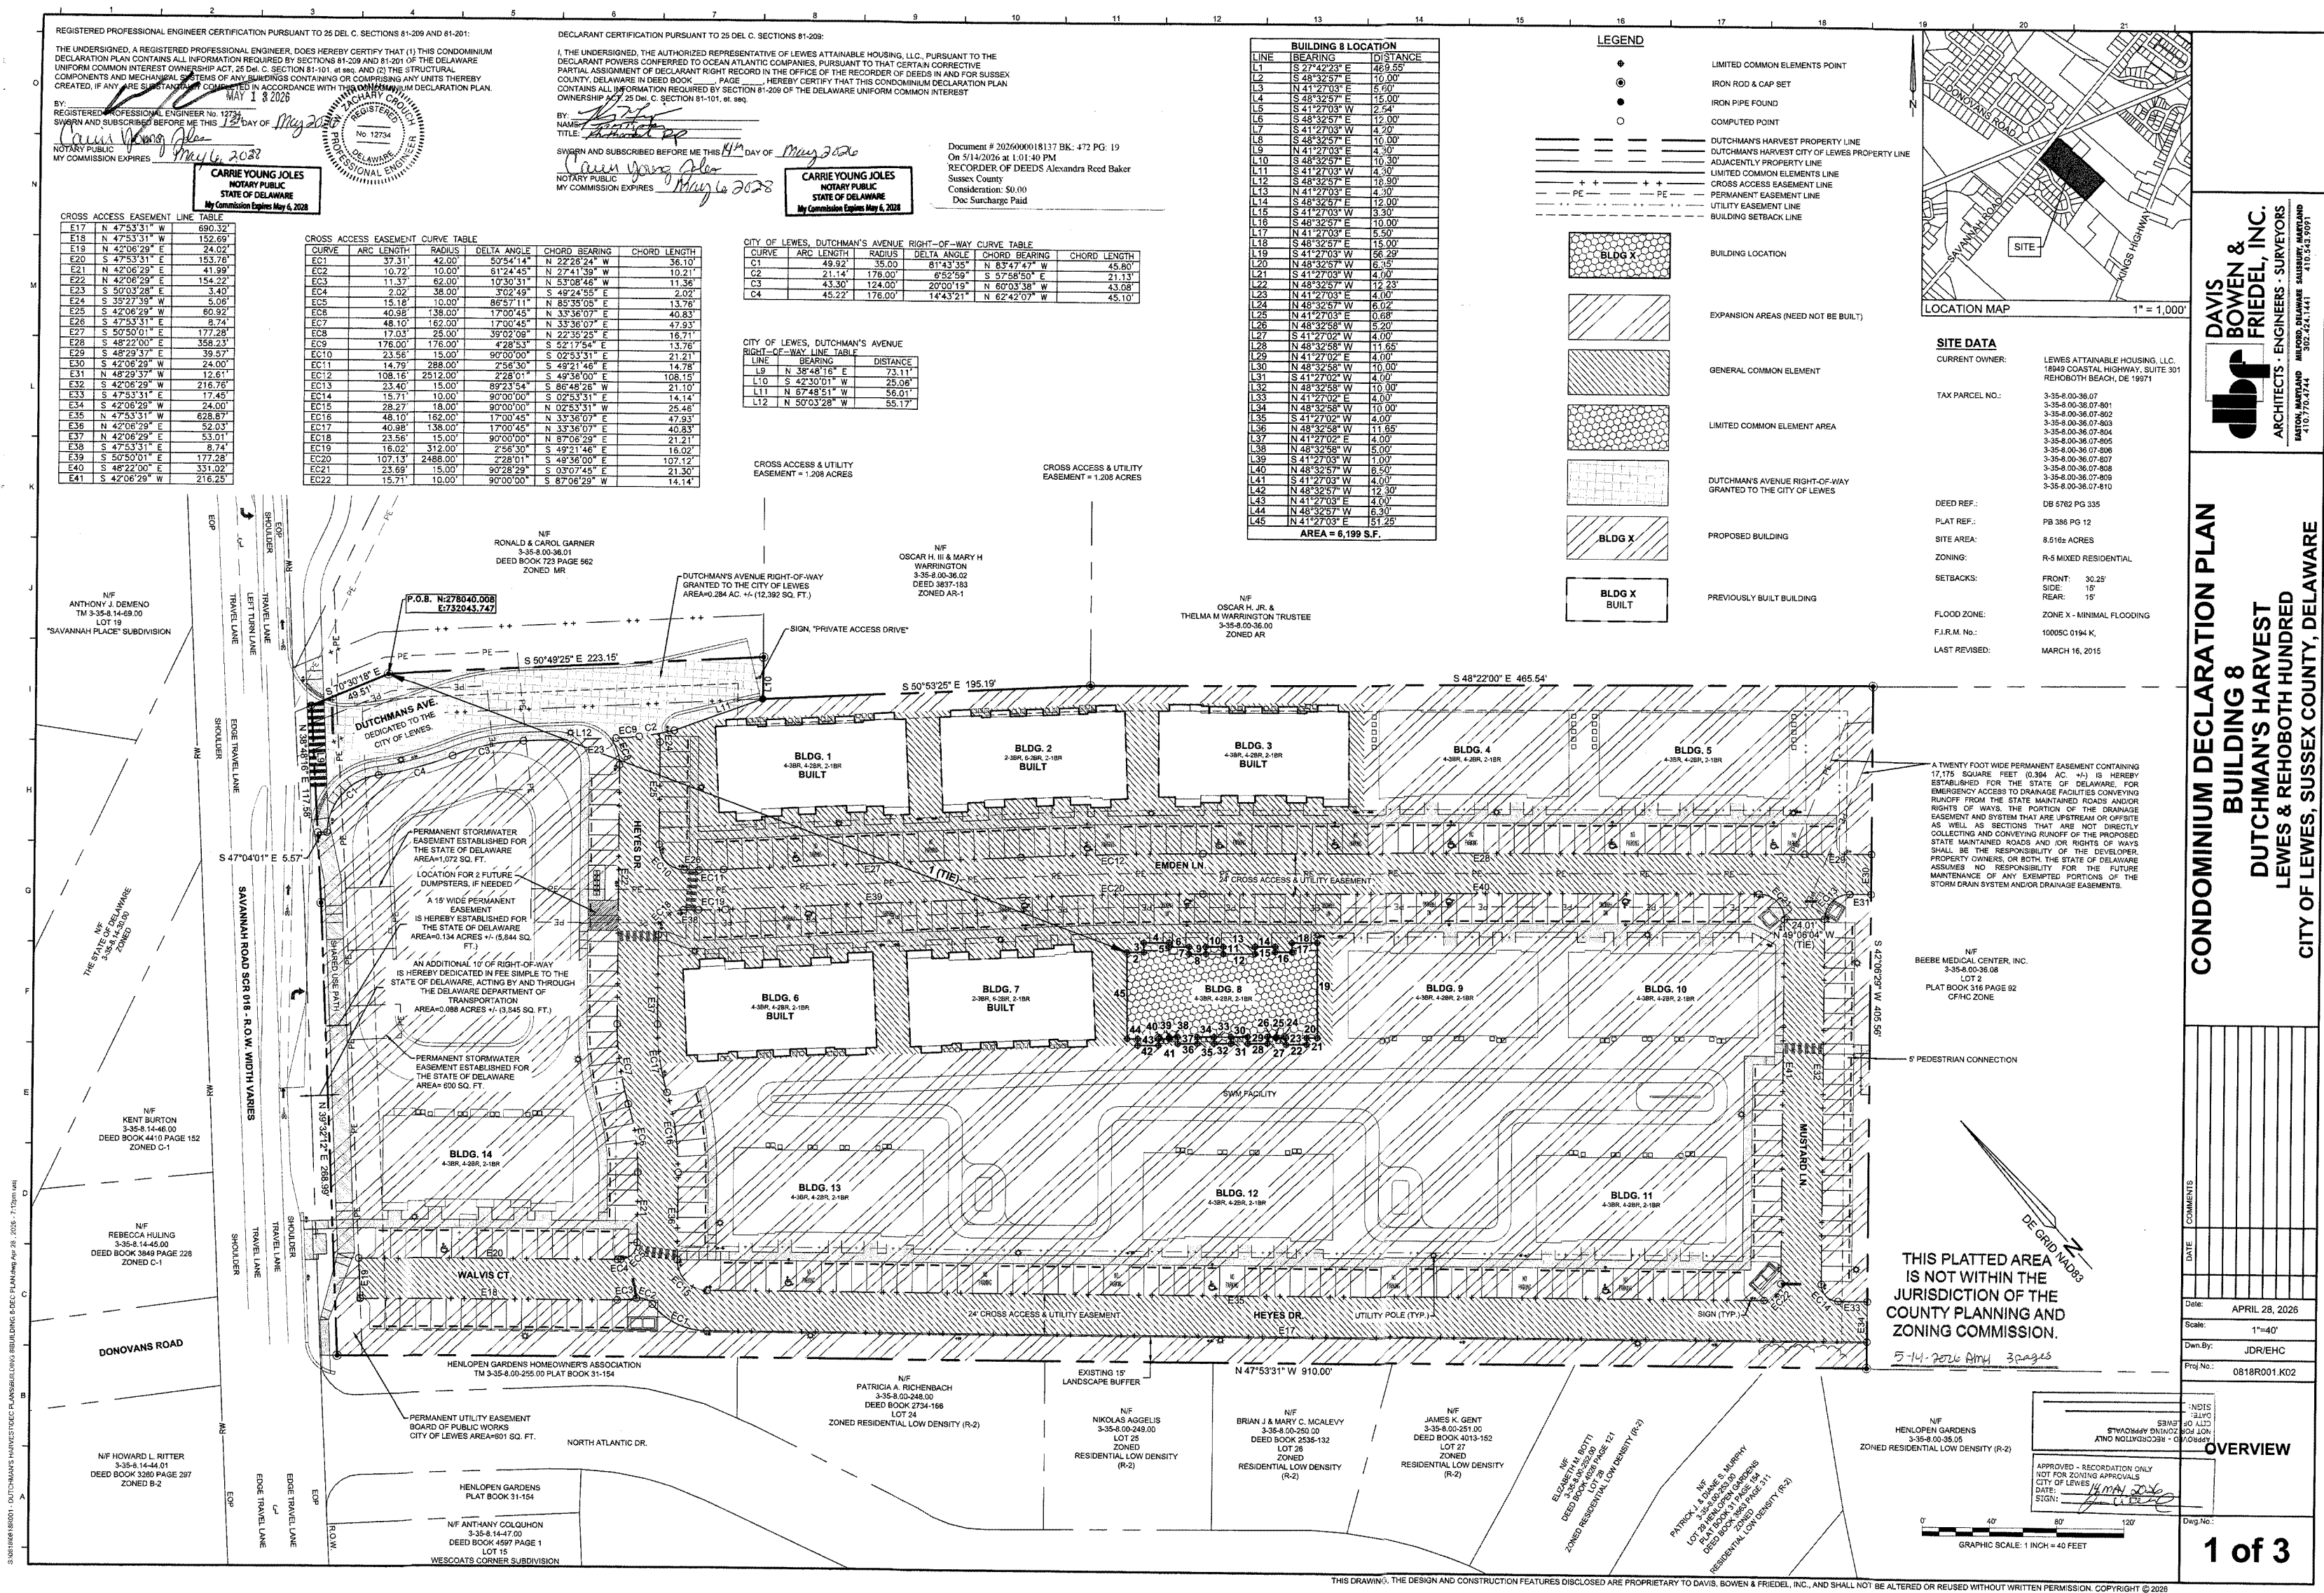
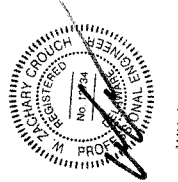


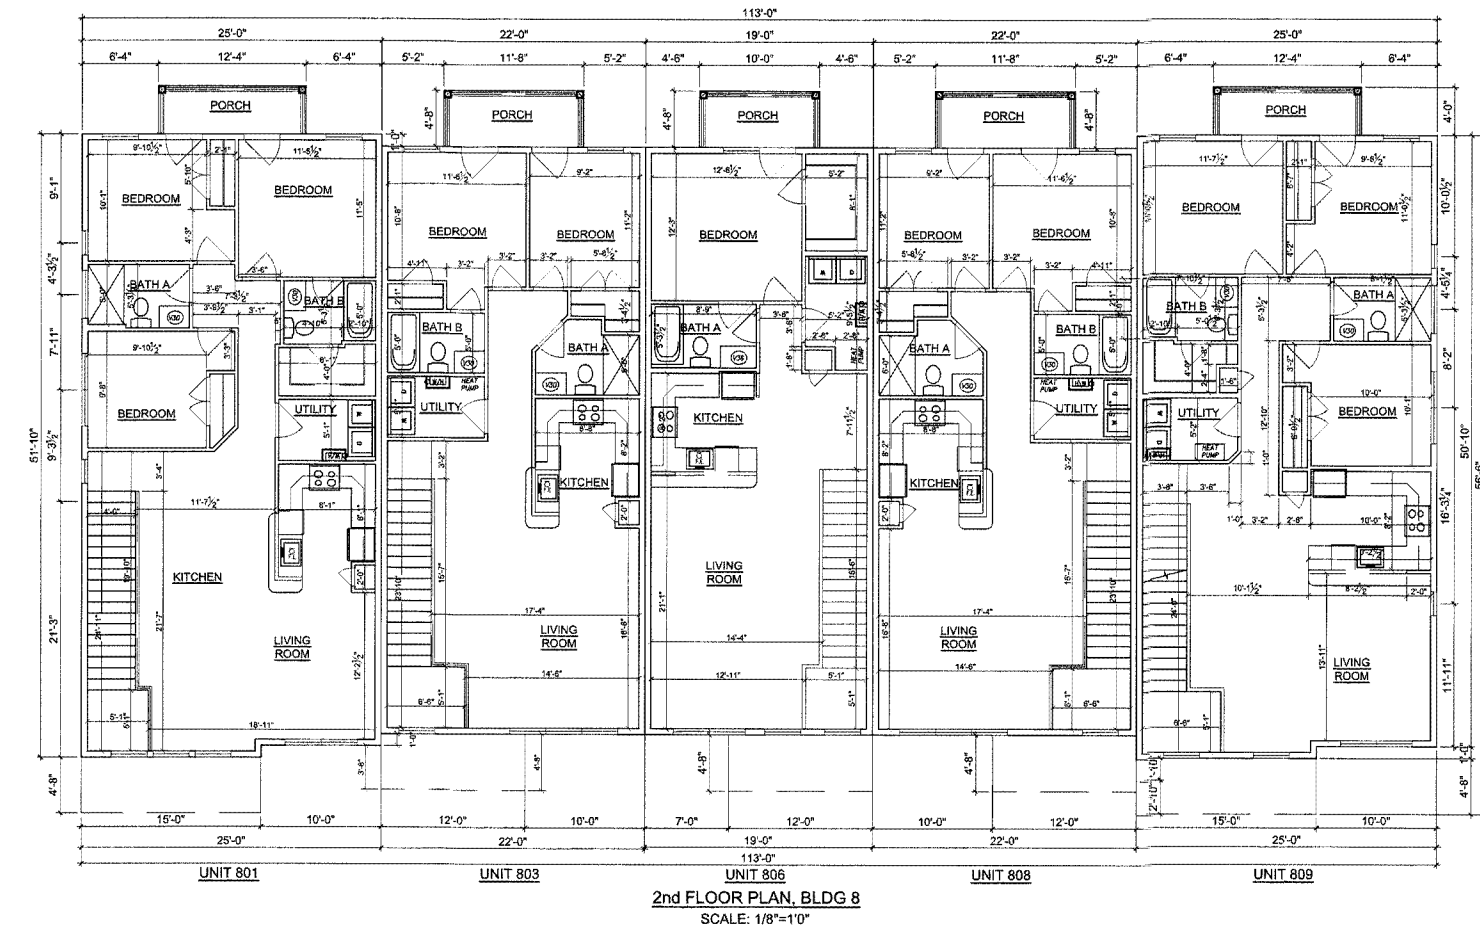

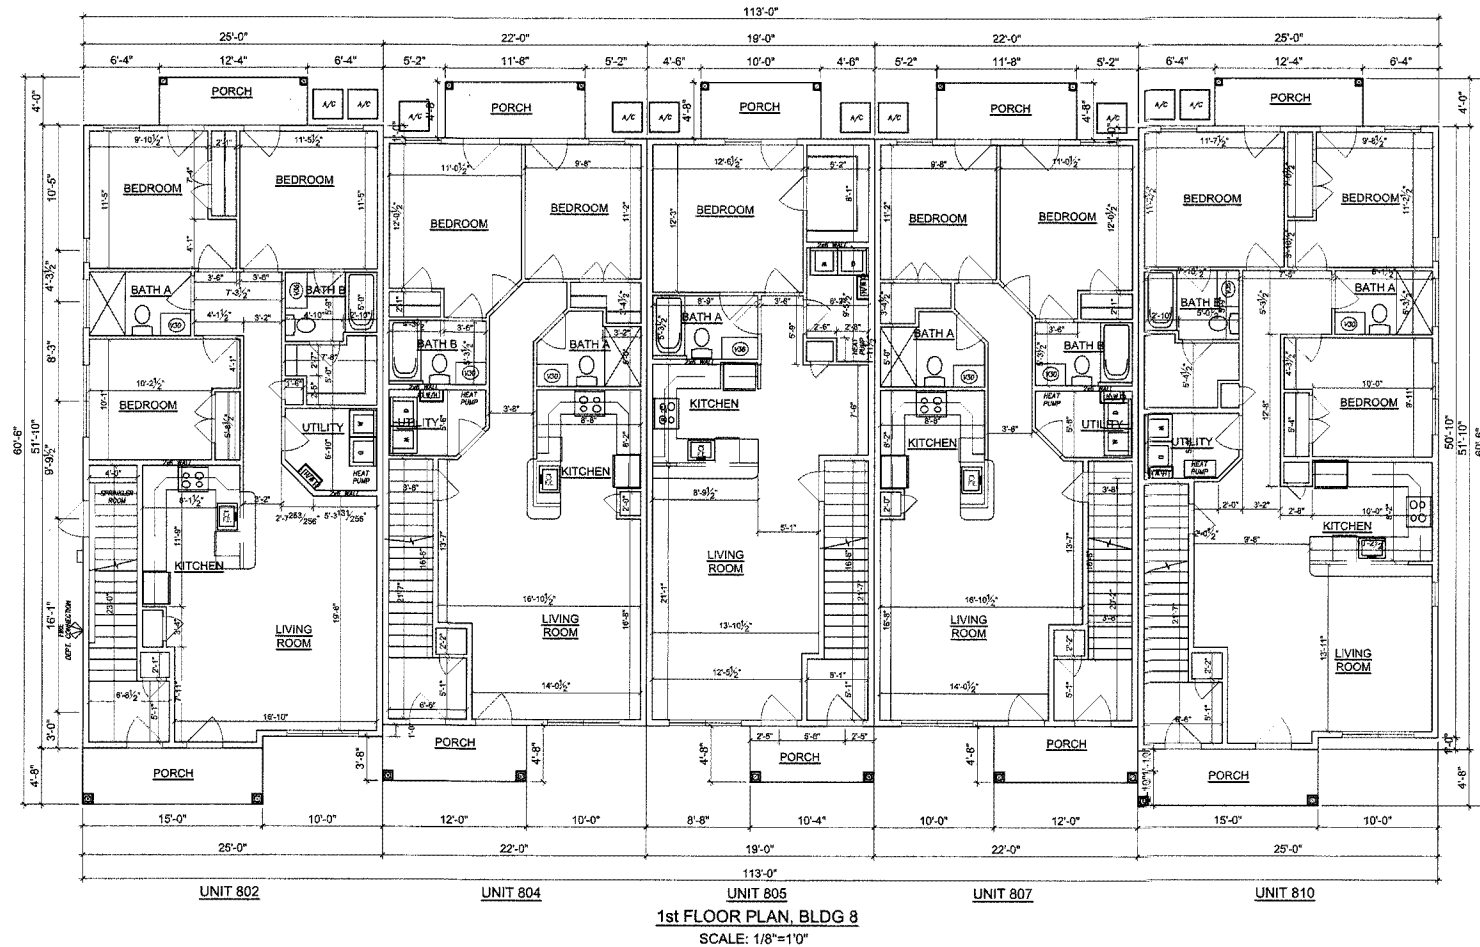







**DAVIS
BOWEN &
FRIEDEL, INC.**
ARCHITECTS - ENGINEERS - SURVEYORS
MILFORD, DELAWARE 19967-1411
410.770.7474

CONDOMINIUM DECLARATION PLAN
BUILDING 8
DUTCHMAN'S HARVEST
LEWES & REHOBOTH HUNDRED
CITY OF LEWES, SUSSEX COUNTY, DELAWARE

DATE	COMMENTS

Date: APRIL 28, 2026
Scale: AS SHOWN
Dwn.By: JDR/EHC
Proj.No.: 0818R001.K02

FLOOR PLANS

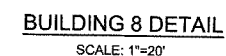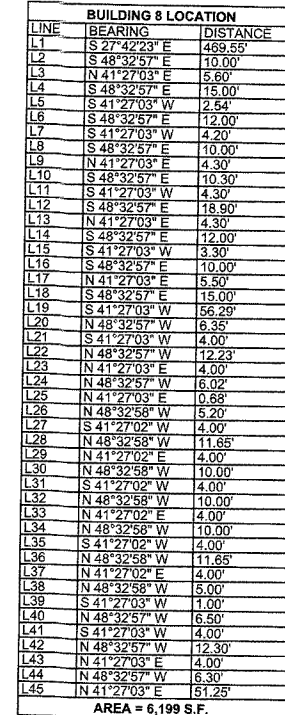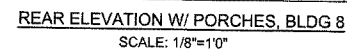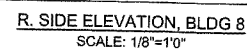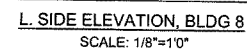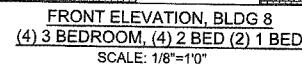



**DAVIS
BOWEN &
FRIEDEL, INC.**

ARCHITECTS - ENGINEERS - SURVEYORS

ASTON, MARYLAND
 410.470.4744
 302.424.1441
 410.463.9001

MAY 1 3 2028



**CONDOMINIUM DECLARATION PLAN
BUILDING 8
DUTCHMAN'S HARVEST
LEWES & REHOBOTH HUNDRED
CITY OF LEWES, SUSSEX COUNTY, DELAWARE**

	DATE	COMMENTS
Date:	APRIL 28, 2026	
Scale:	AS SHOWN	
Dwn.By:	EHC	
Proj No.:	0818R001.K02	

ELEVATIONS & DETAIL