




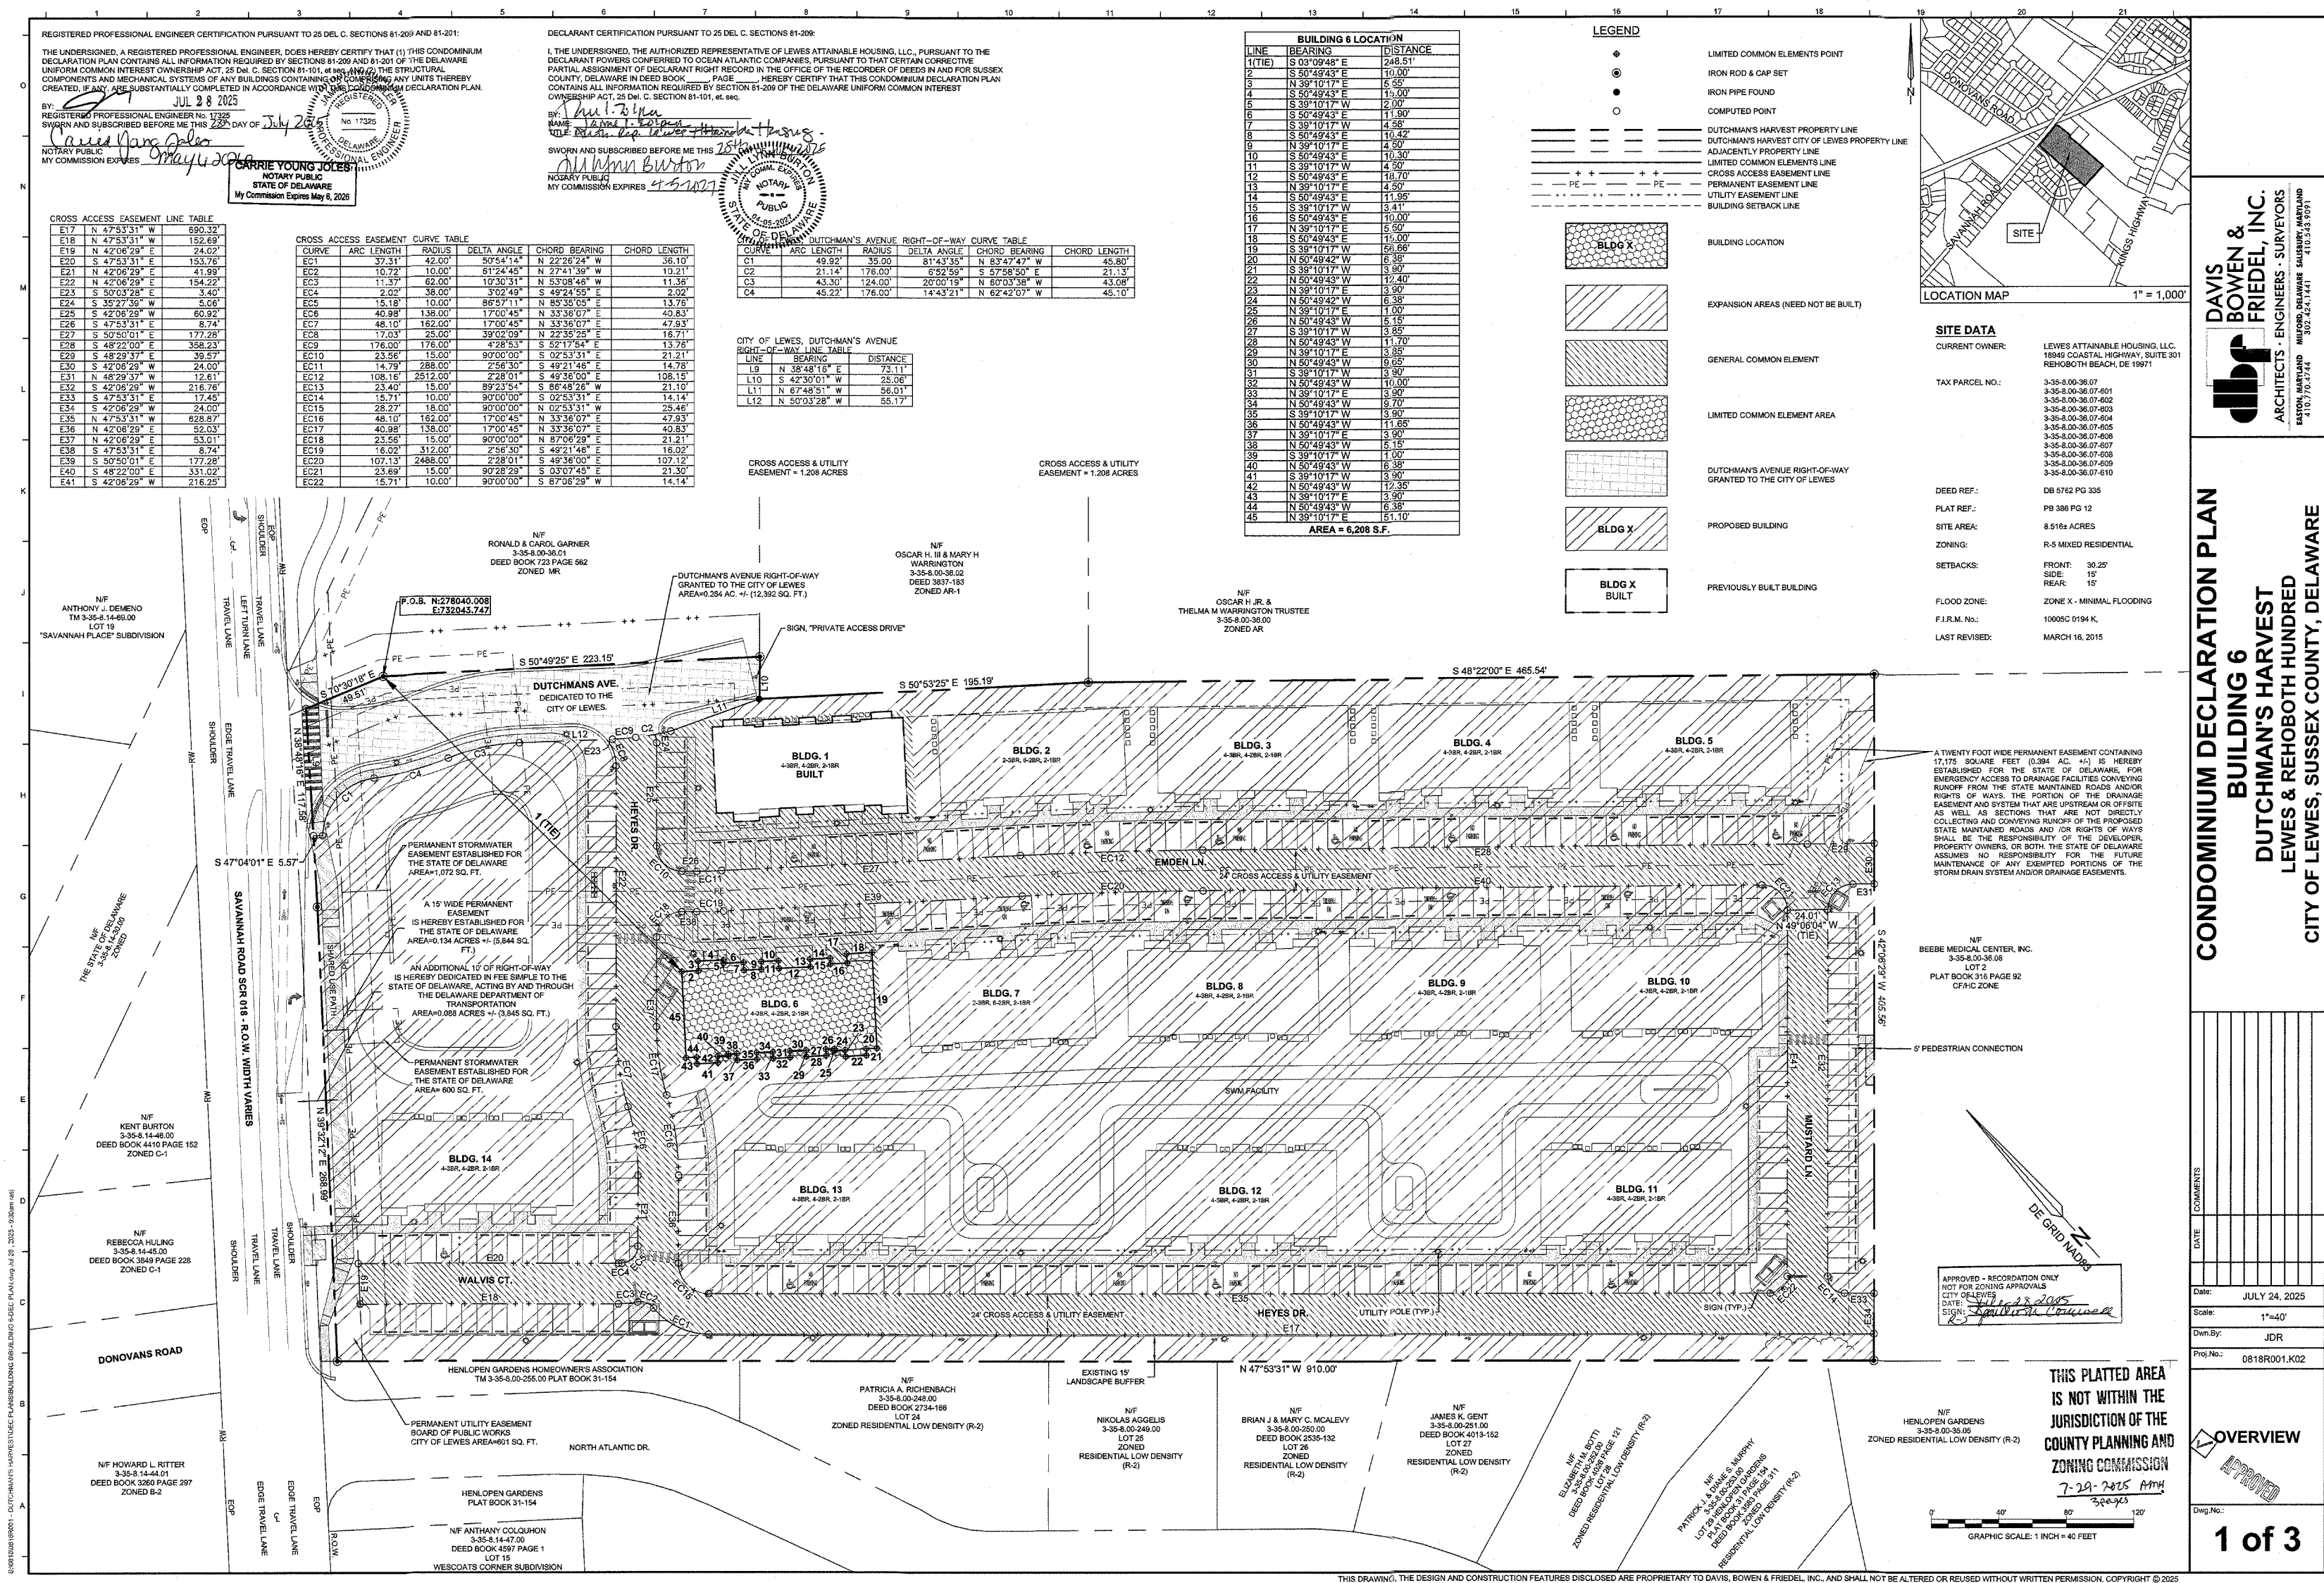

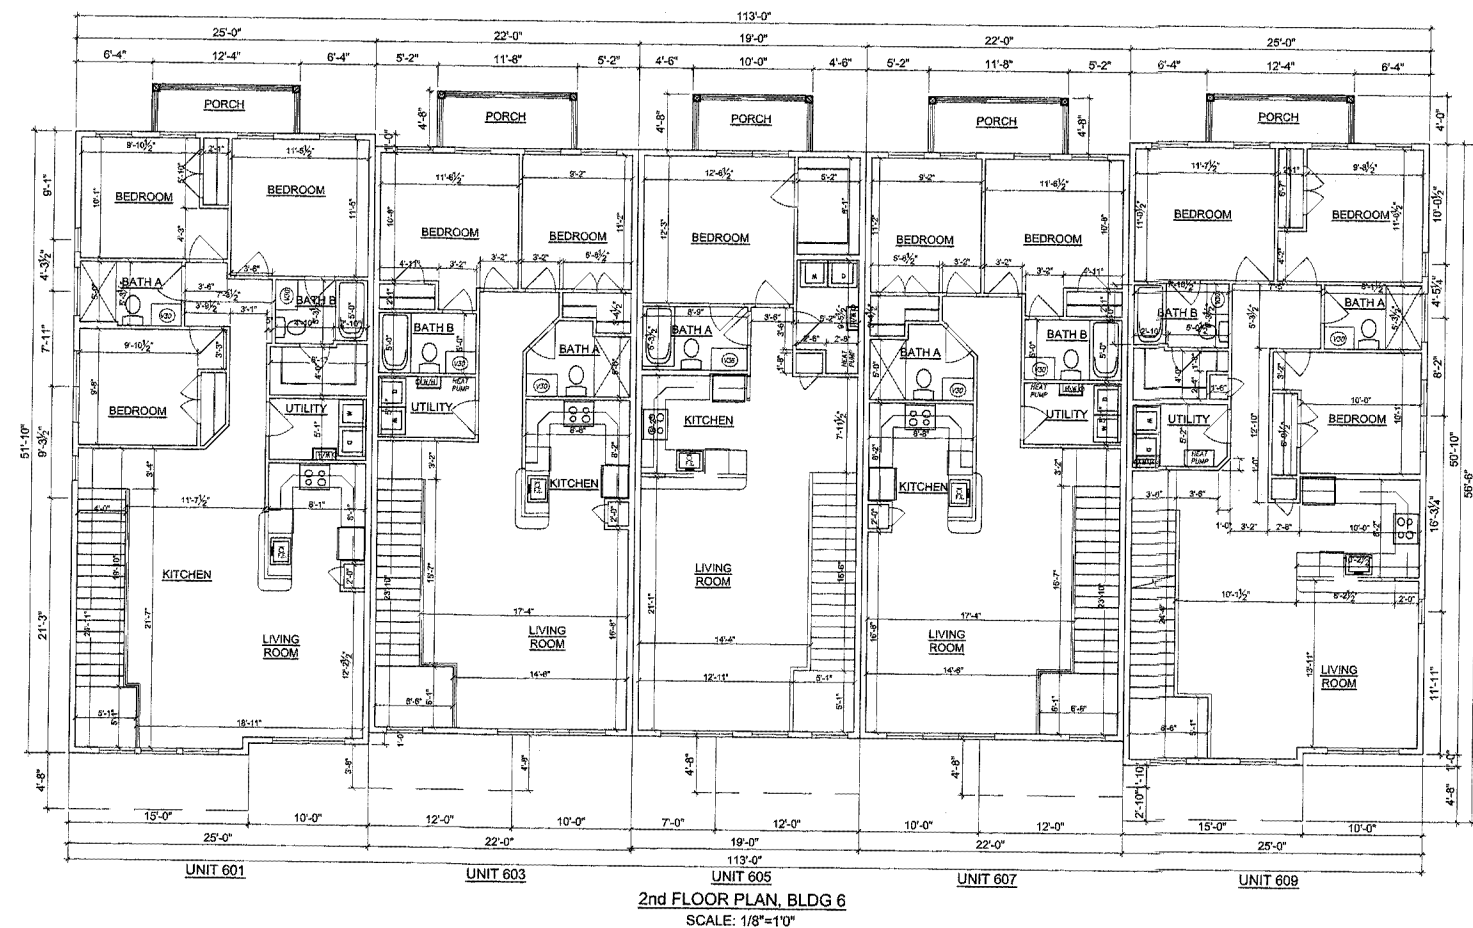

THIS DRAWING, THE DESIGN AND CONSTRUCTION FEATURES DISCLOSED ARE PROPRIETARY TO DAVIS, BOWEN & FRIEDEL, INC., AND SHALL NOT BE ALTERED OR REUSED WITHOUT WRITTEN PERMISSION. COPYRIGHT © 2025

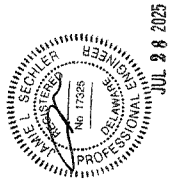

**DAVIS
BOWEN &
FRIEDEL, INC.**

dbf

ARCHITECTS • ENGINEERS • SURVEYORS

EASTON, MARYLAND
410.770.4744

MILFORD, DELAWARE
302.424.1441

SALISBURY, MARYLAND
410.543.2091








**CONDOMINIUM DECLARATION PLAN
BUILDING 6
DUTCHMAN'S HARVEST
LEWES & REHOBOTH HUNDRED
CITY OF LEWES, SUSSEX COUNTY, DELAWARE**

[illegible]

FLOOR PLANS

☒ APPROVED

Dwg.No.:

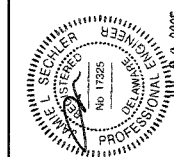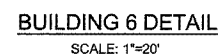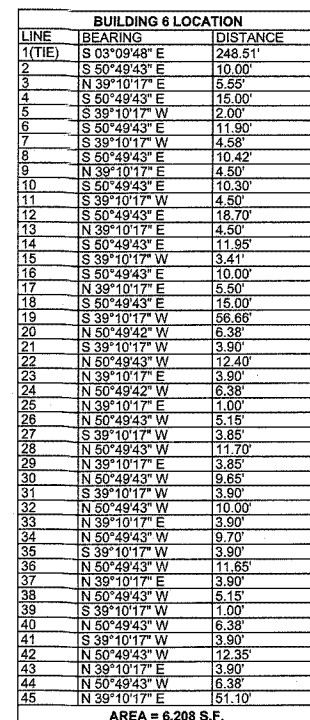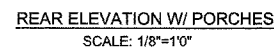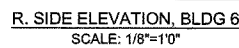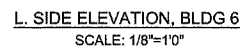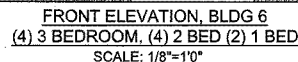

dbf **DAVIS BOWEN & FRIEDEL, INC.**
ARCHITECTS • ENGINEERS • SURVEYORS
BALTIMORE, MARYLAND WILMINGTON, DELAWARE SALISBURY, MARYLAND

**CONDOMINIUM DECLARATION PLAN
BUILDING 6
DUTCHMAN'S HARVEST
LEWES & REHOBOTH HUNDRED
CITY OF LEWES, SUSSEX COUNTY, DELAWARE**

[illegible]

Date: 11/11/2025

Scale: AS SHOWN

Dwn.By: IDP

Proj.No.:	0813D001 K02
-----------	--------------

**ELEVATIONS
& DETAIL**

Dwg.No.: