



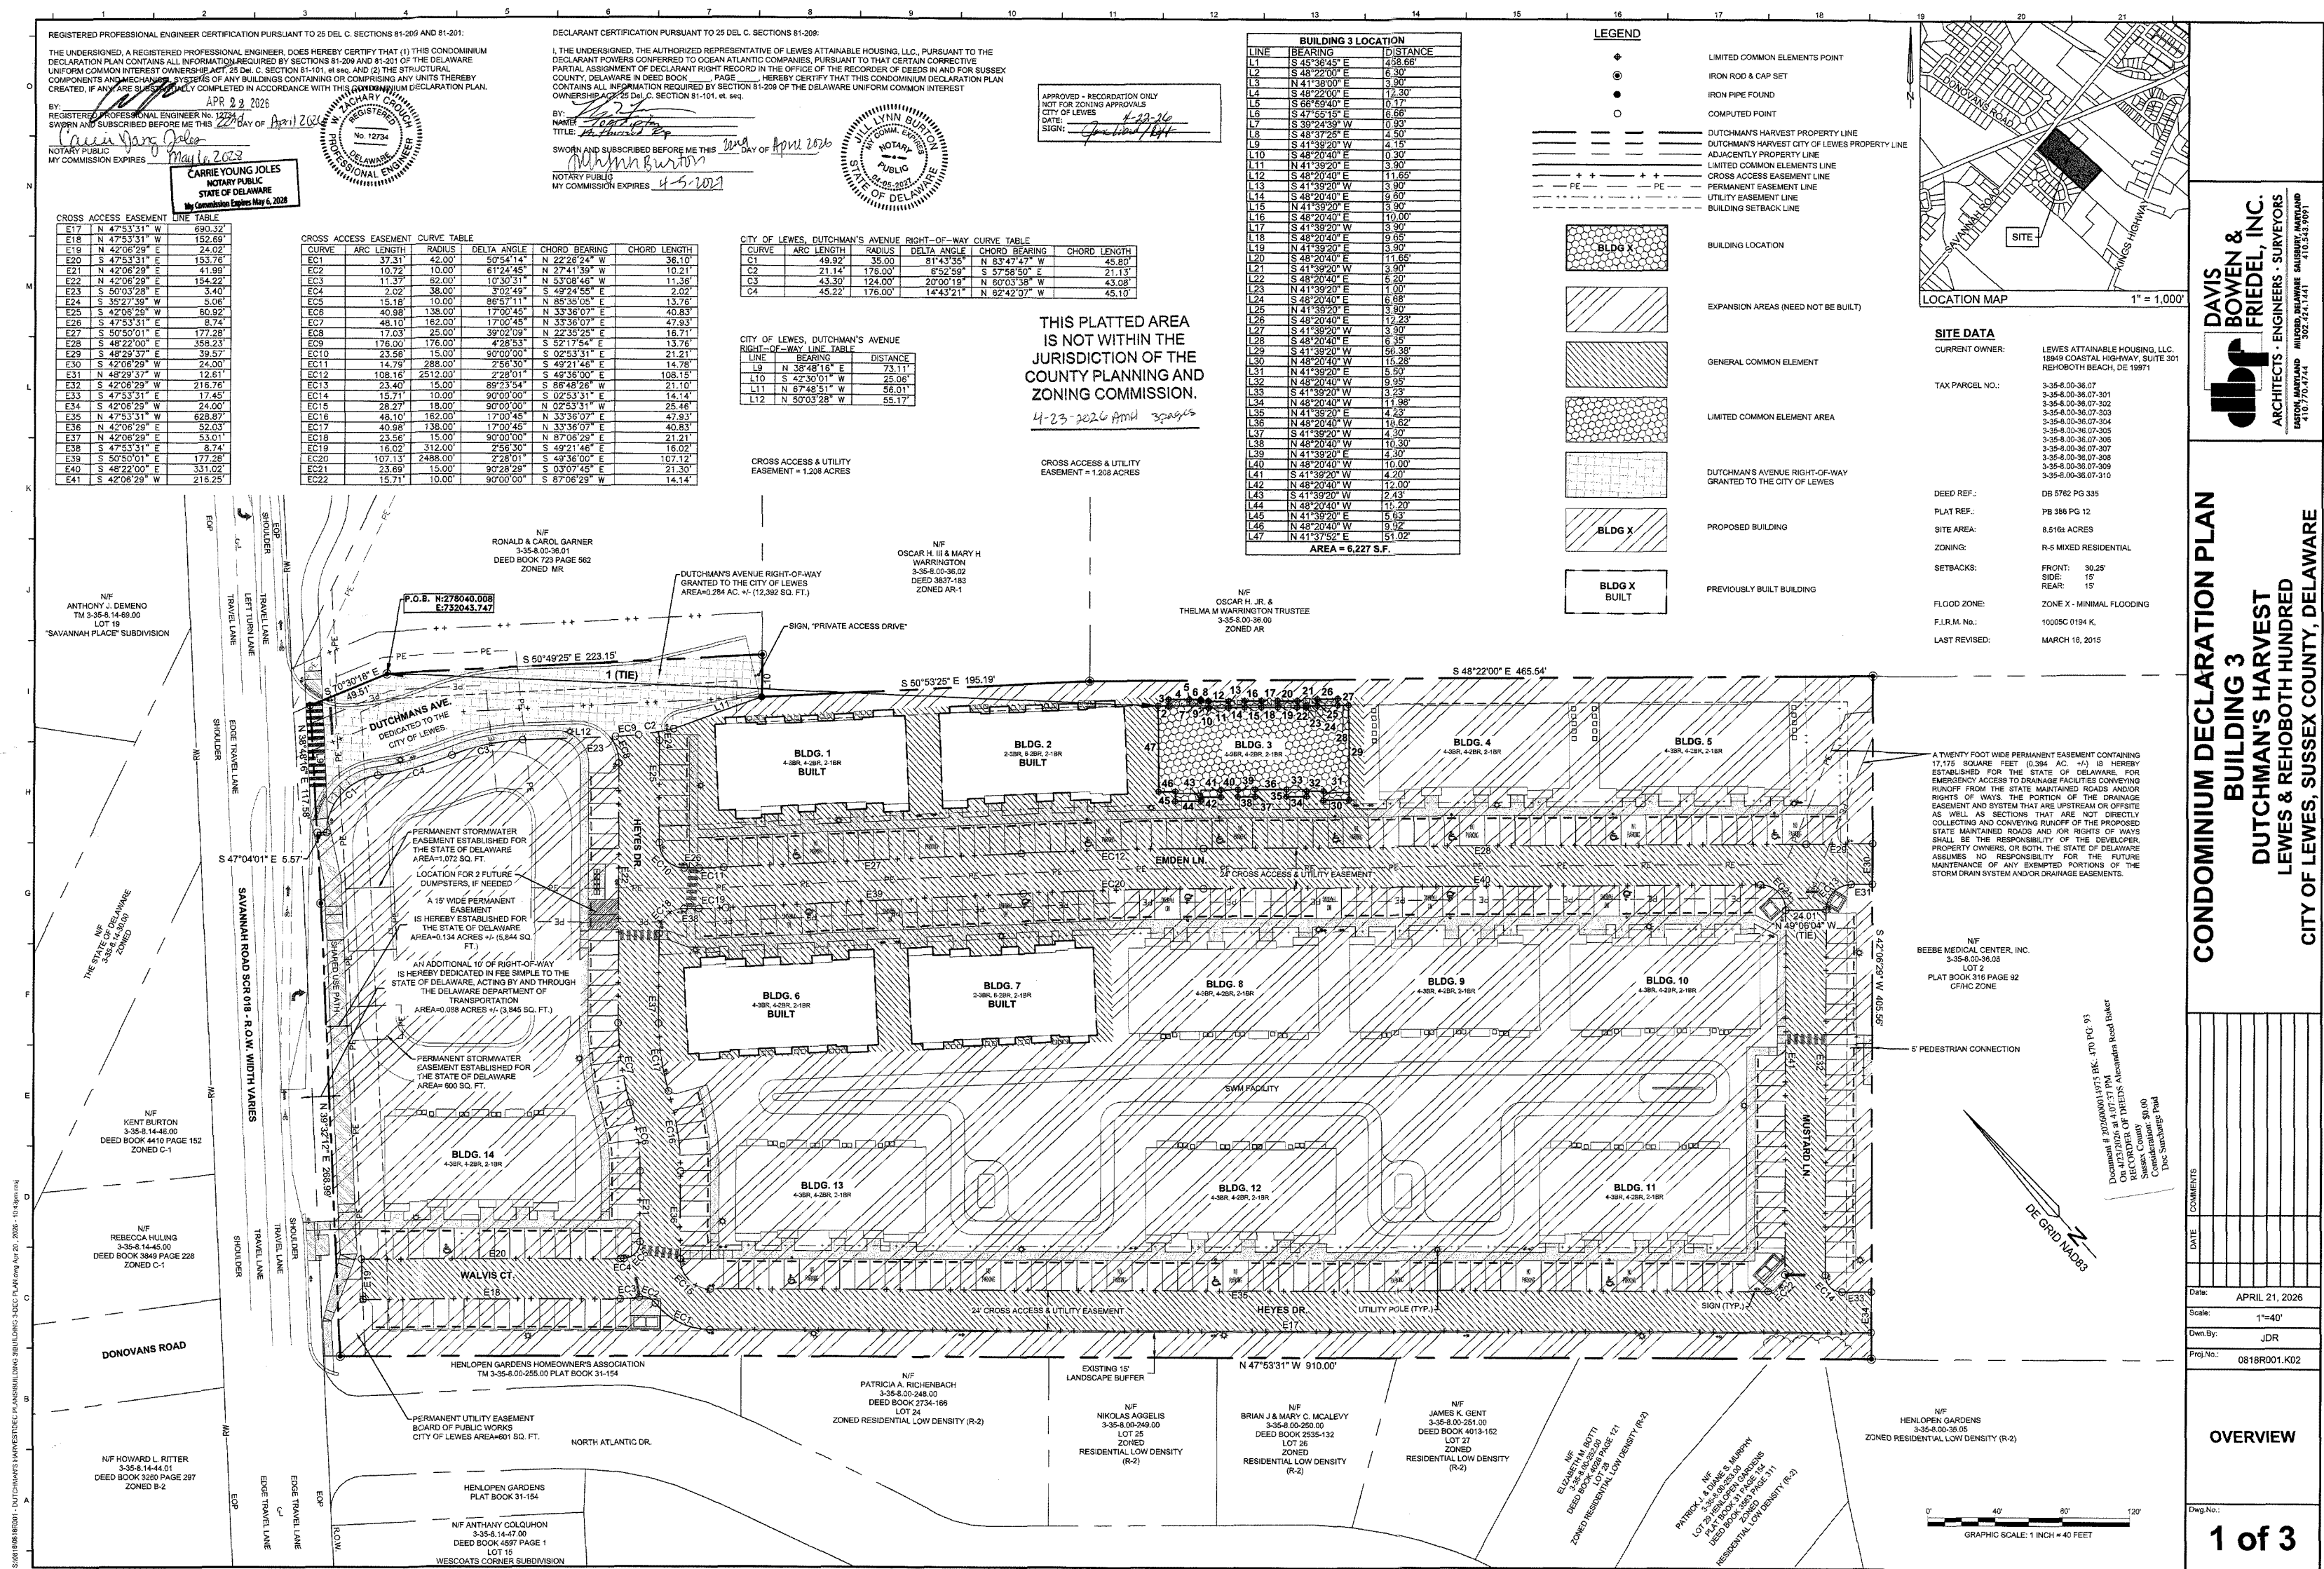

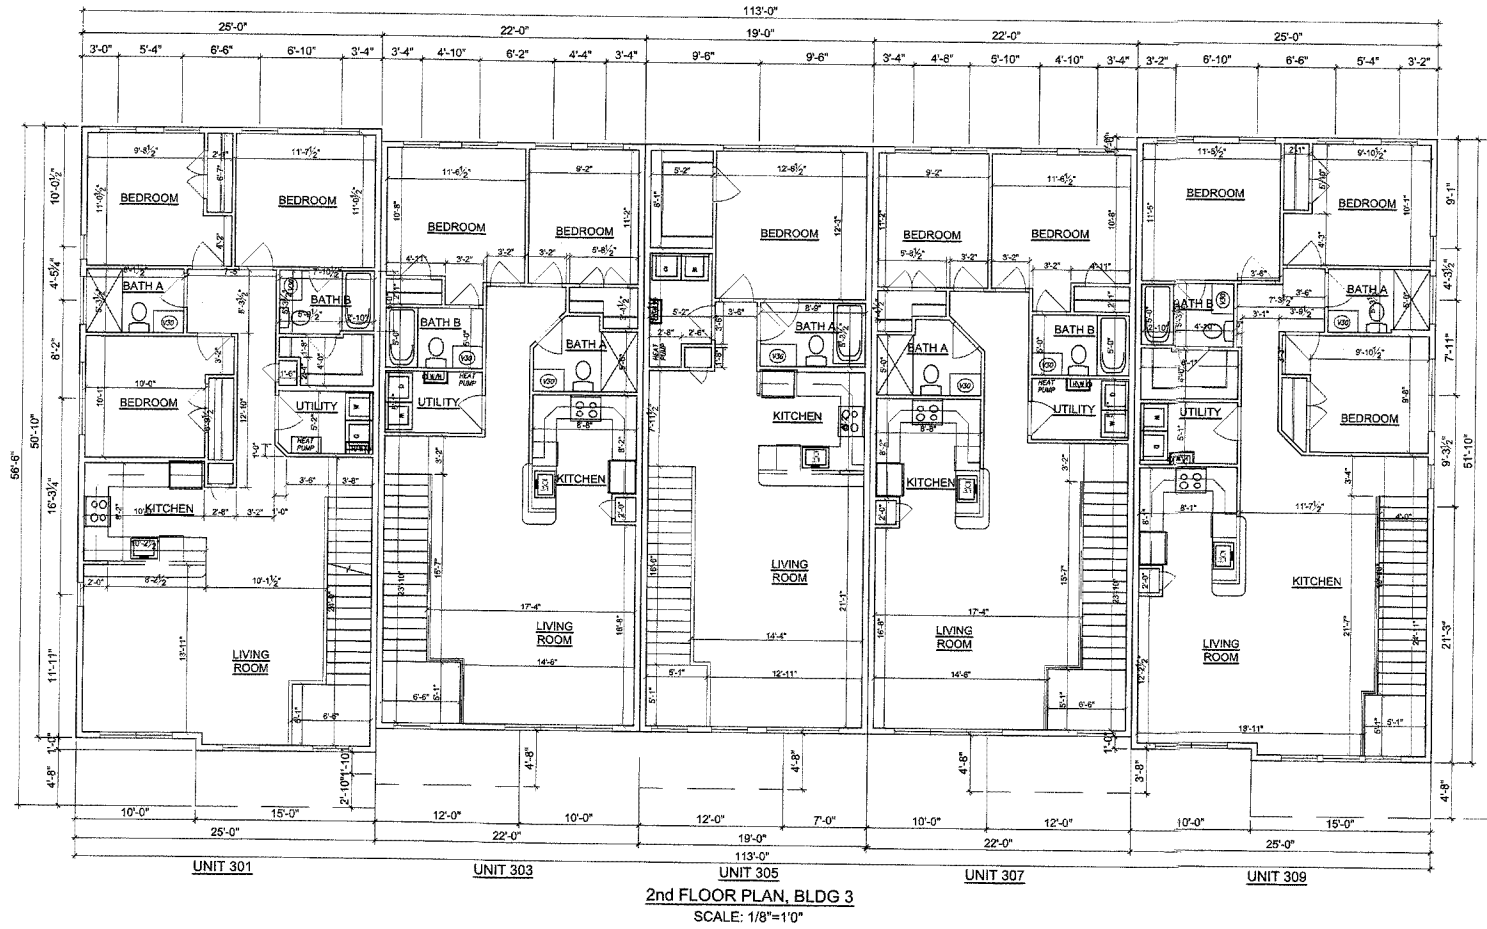

**DAVIS
BOWEN &
FRIEDEL, INC.**

ARCHITECTS • ENGINEERS • SURVEYORS

EASTON, MARYLAND
410.770.4744

MILFORD, DELAWARE
302.424.1441

SALISBURY, MARYLAND
410.543.9091

CONDOMINIUM DECLARATION PLAN
BUILDING 3
DUTCHMAN'S HARVEST
LEWES & REHOBOTH HUNDRED
CITY OF LEWES, SUSSEX COUNTY, DELAWARE

[illegible]

Date:	APRIL 21, 2026
Scale:	AS SHOWN
Dwn.By:	JDR
Proj.No.:	0818R001.K02

FLOOR PLANS

Dwg.No.:
2 of 3

