

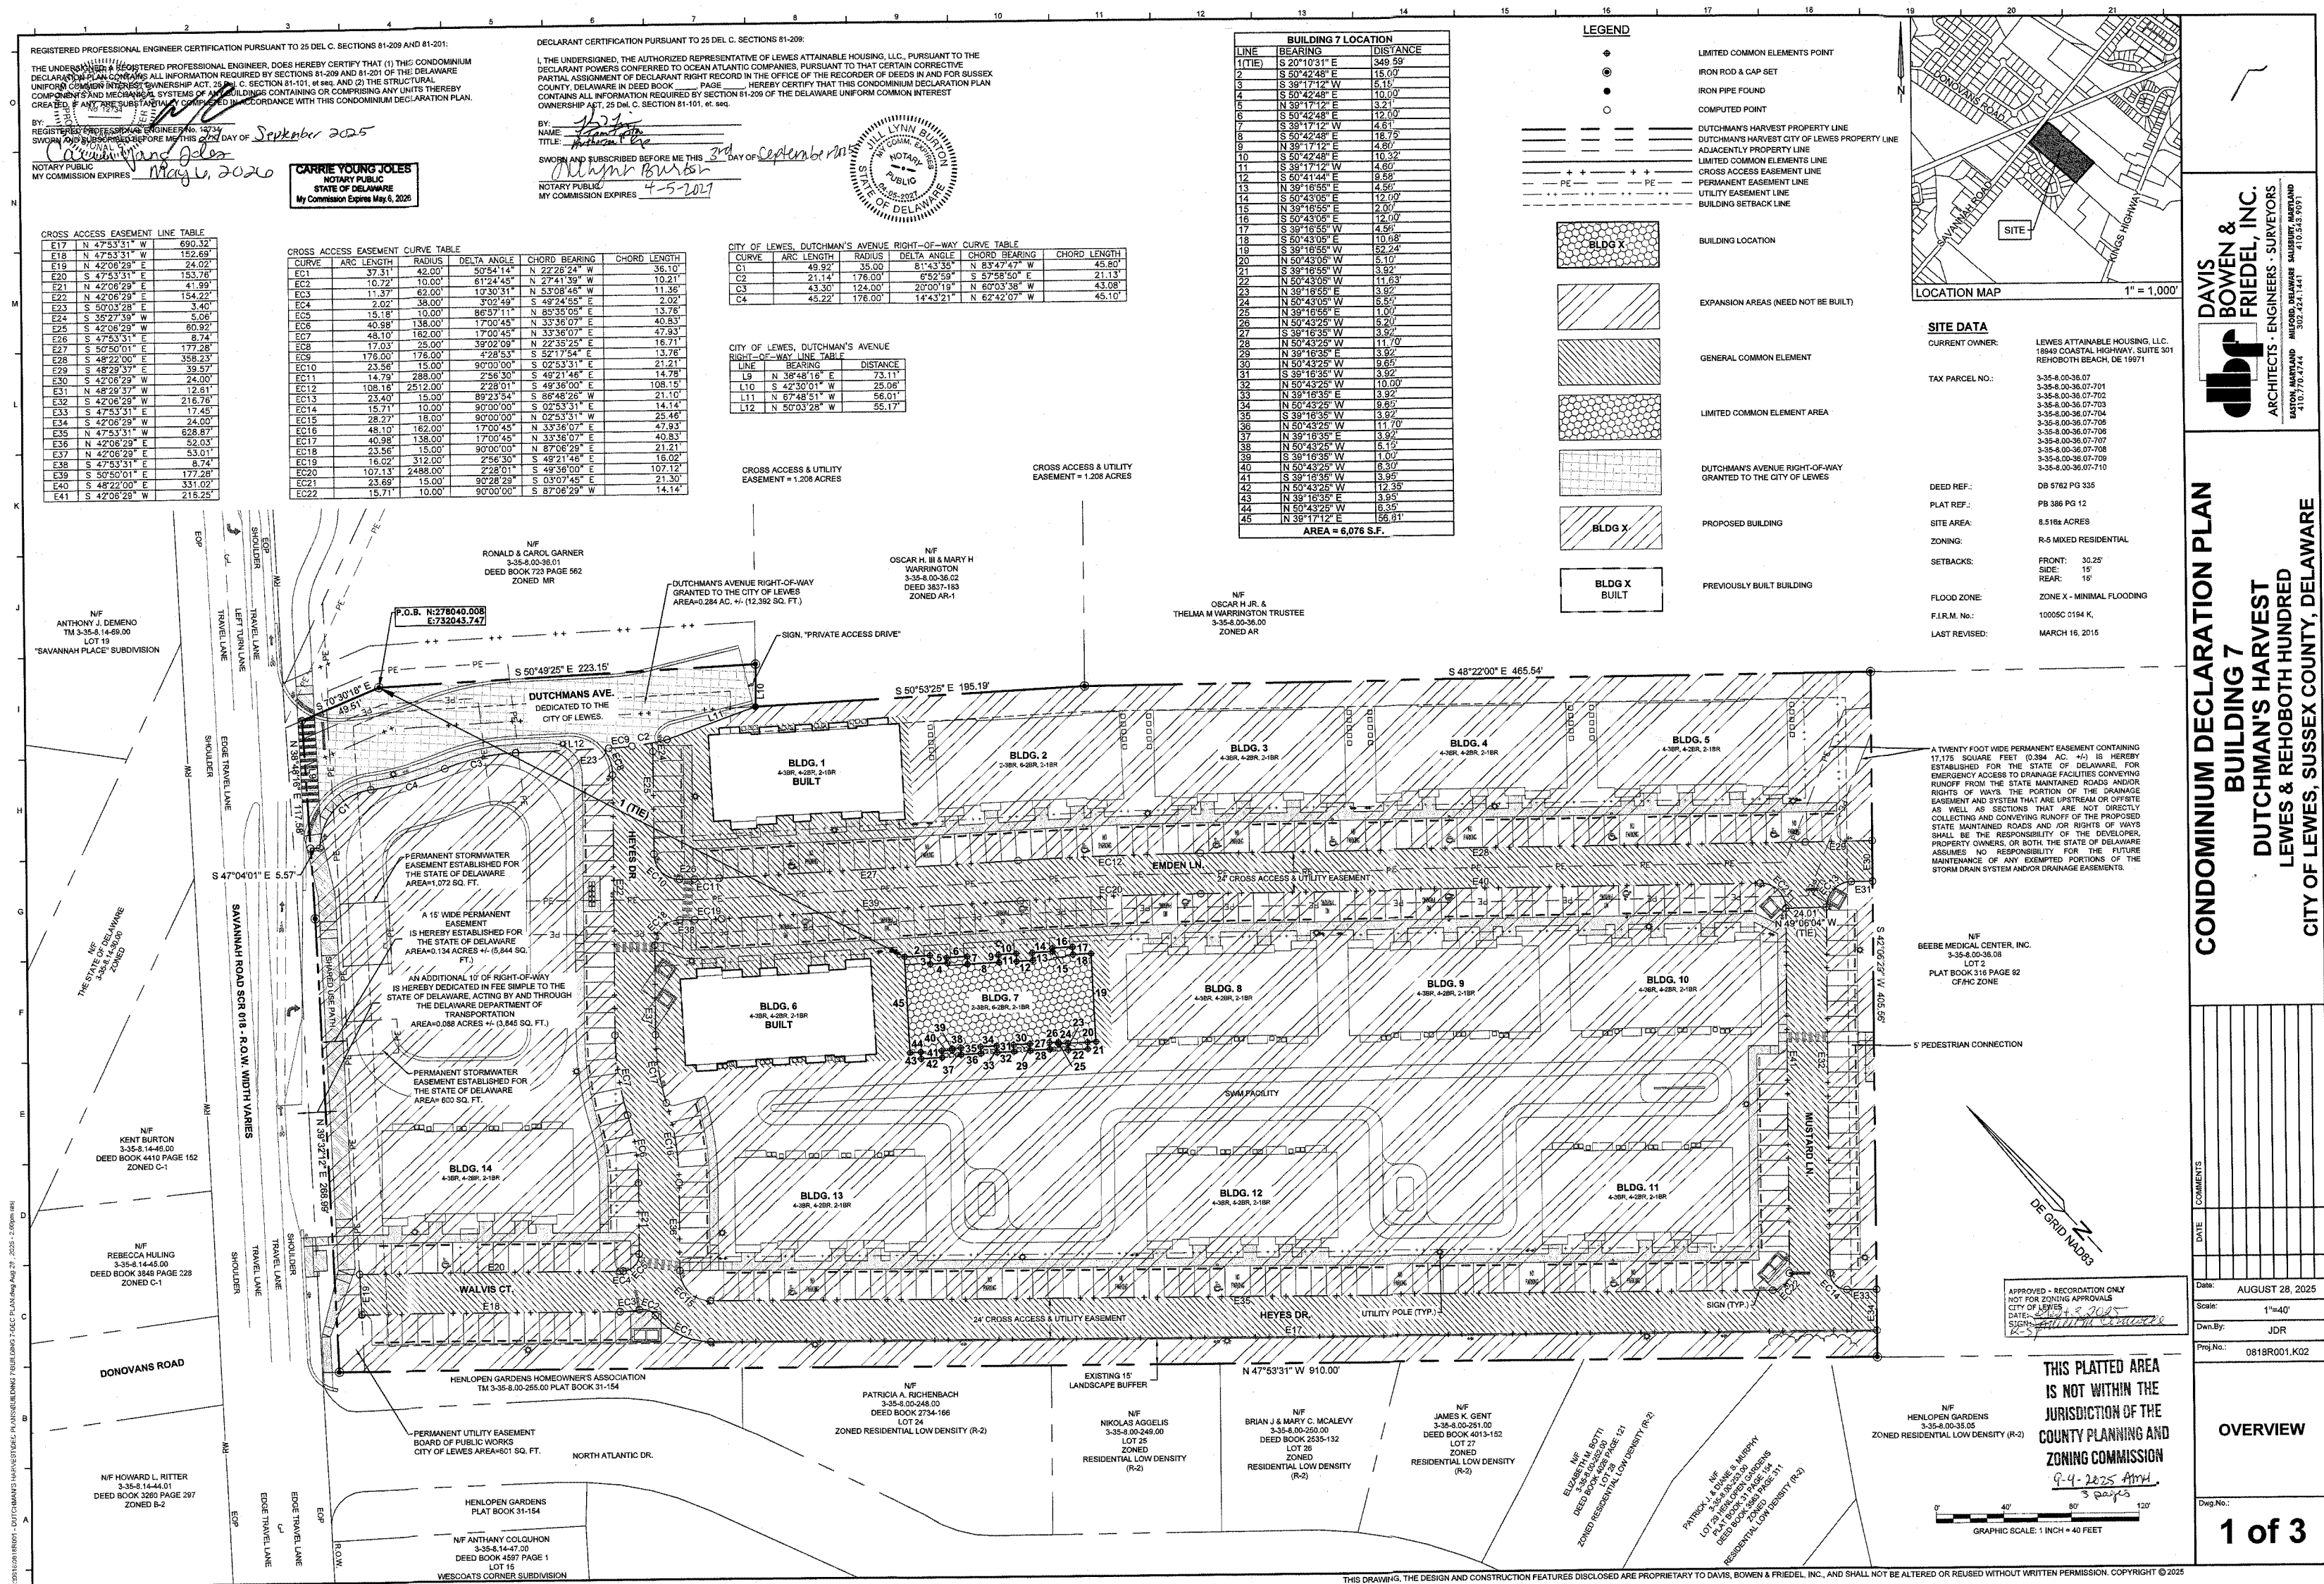


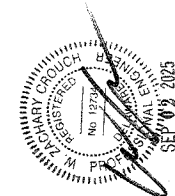

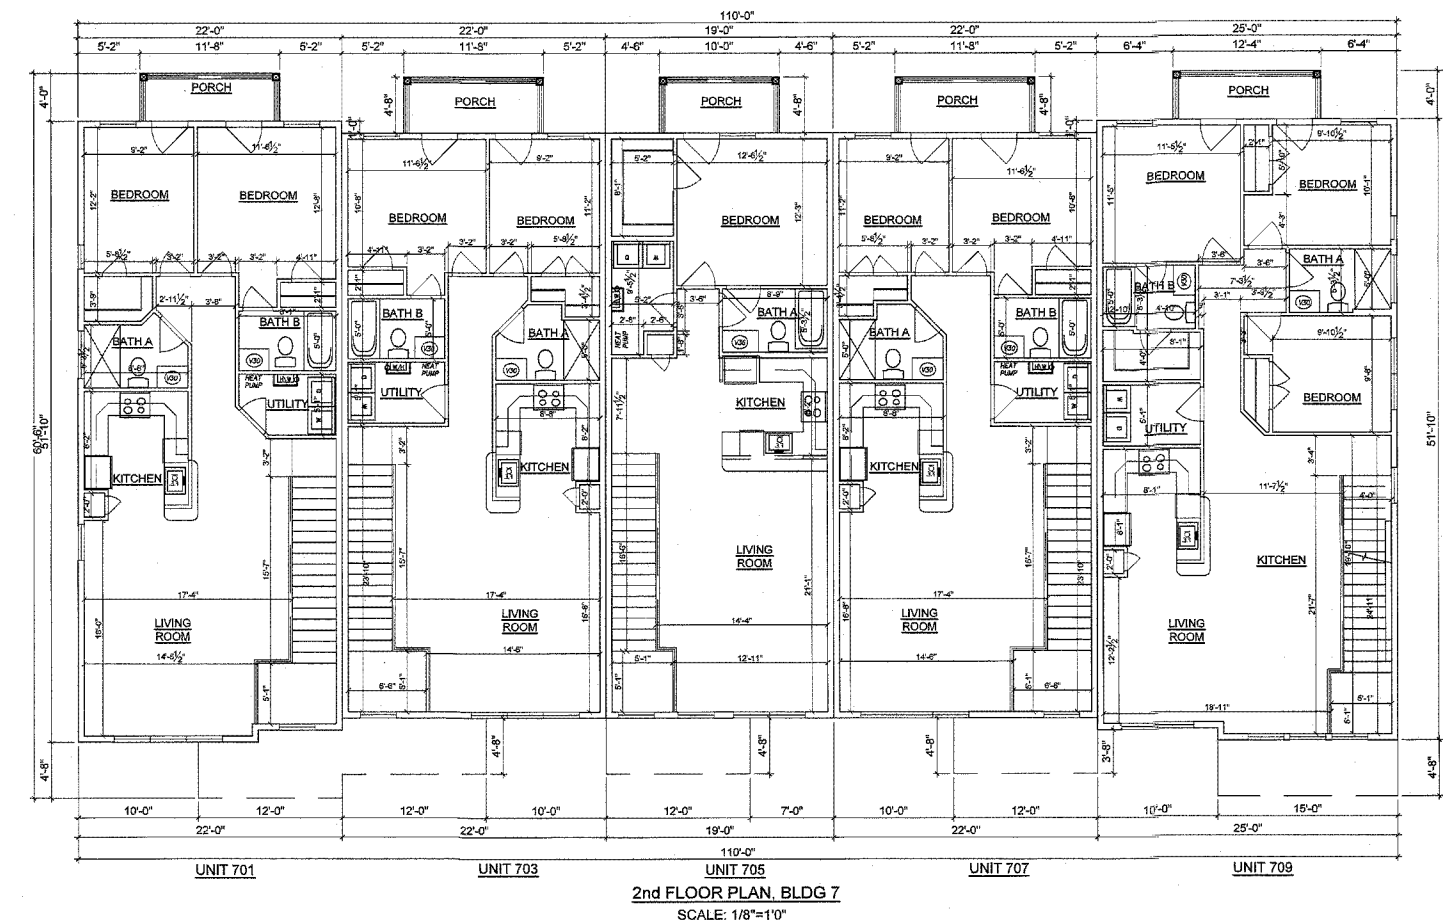

**DAVIS
BOWEN &
FRIEDEL, INC.**

dbf

ARCHITECTS • ENGINEERS • SURVEYORS

BOSTON, MASSACHUSETTS
410.770.4744

MILFORD, DELAWARE
302.424.1441

MARTLAND, VIRGINIA
410.543.7091

**CONDOMINIUM DECLARATION PLAN
BUILDING 7
DUTCHMAN'S HARVEST
LEWES & REHOBOTH HUNDRED
CITY OF LEWES, SUSSEX COUNTY, DELAWARE**

[illegible]

FLOOR PLANS

Dwg.No.:
2 of 3

