

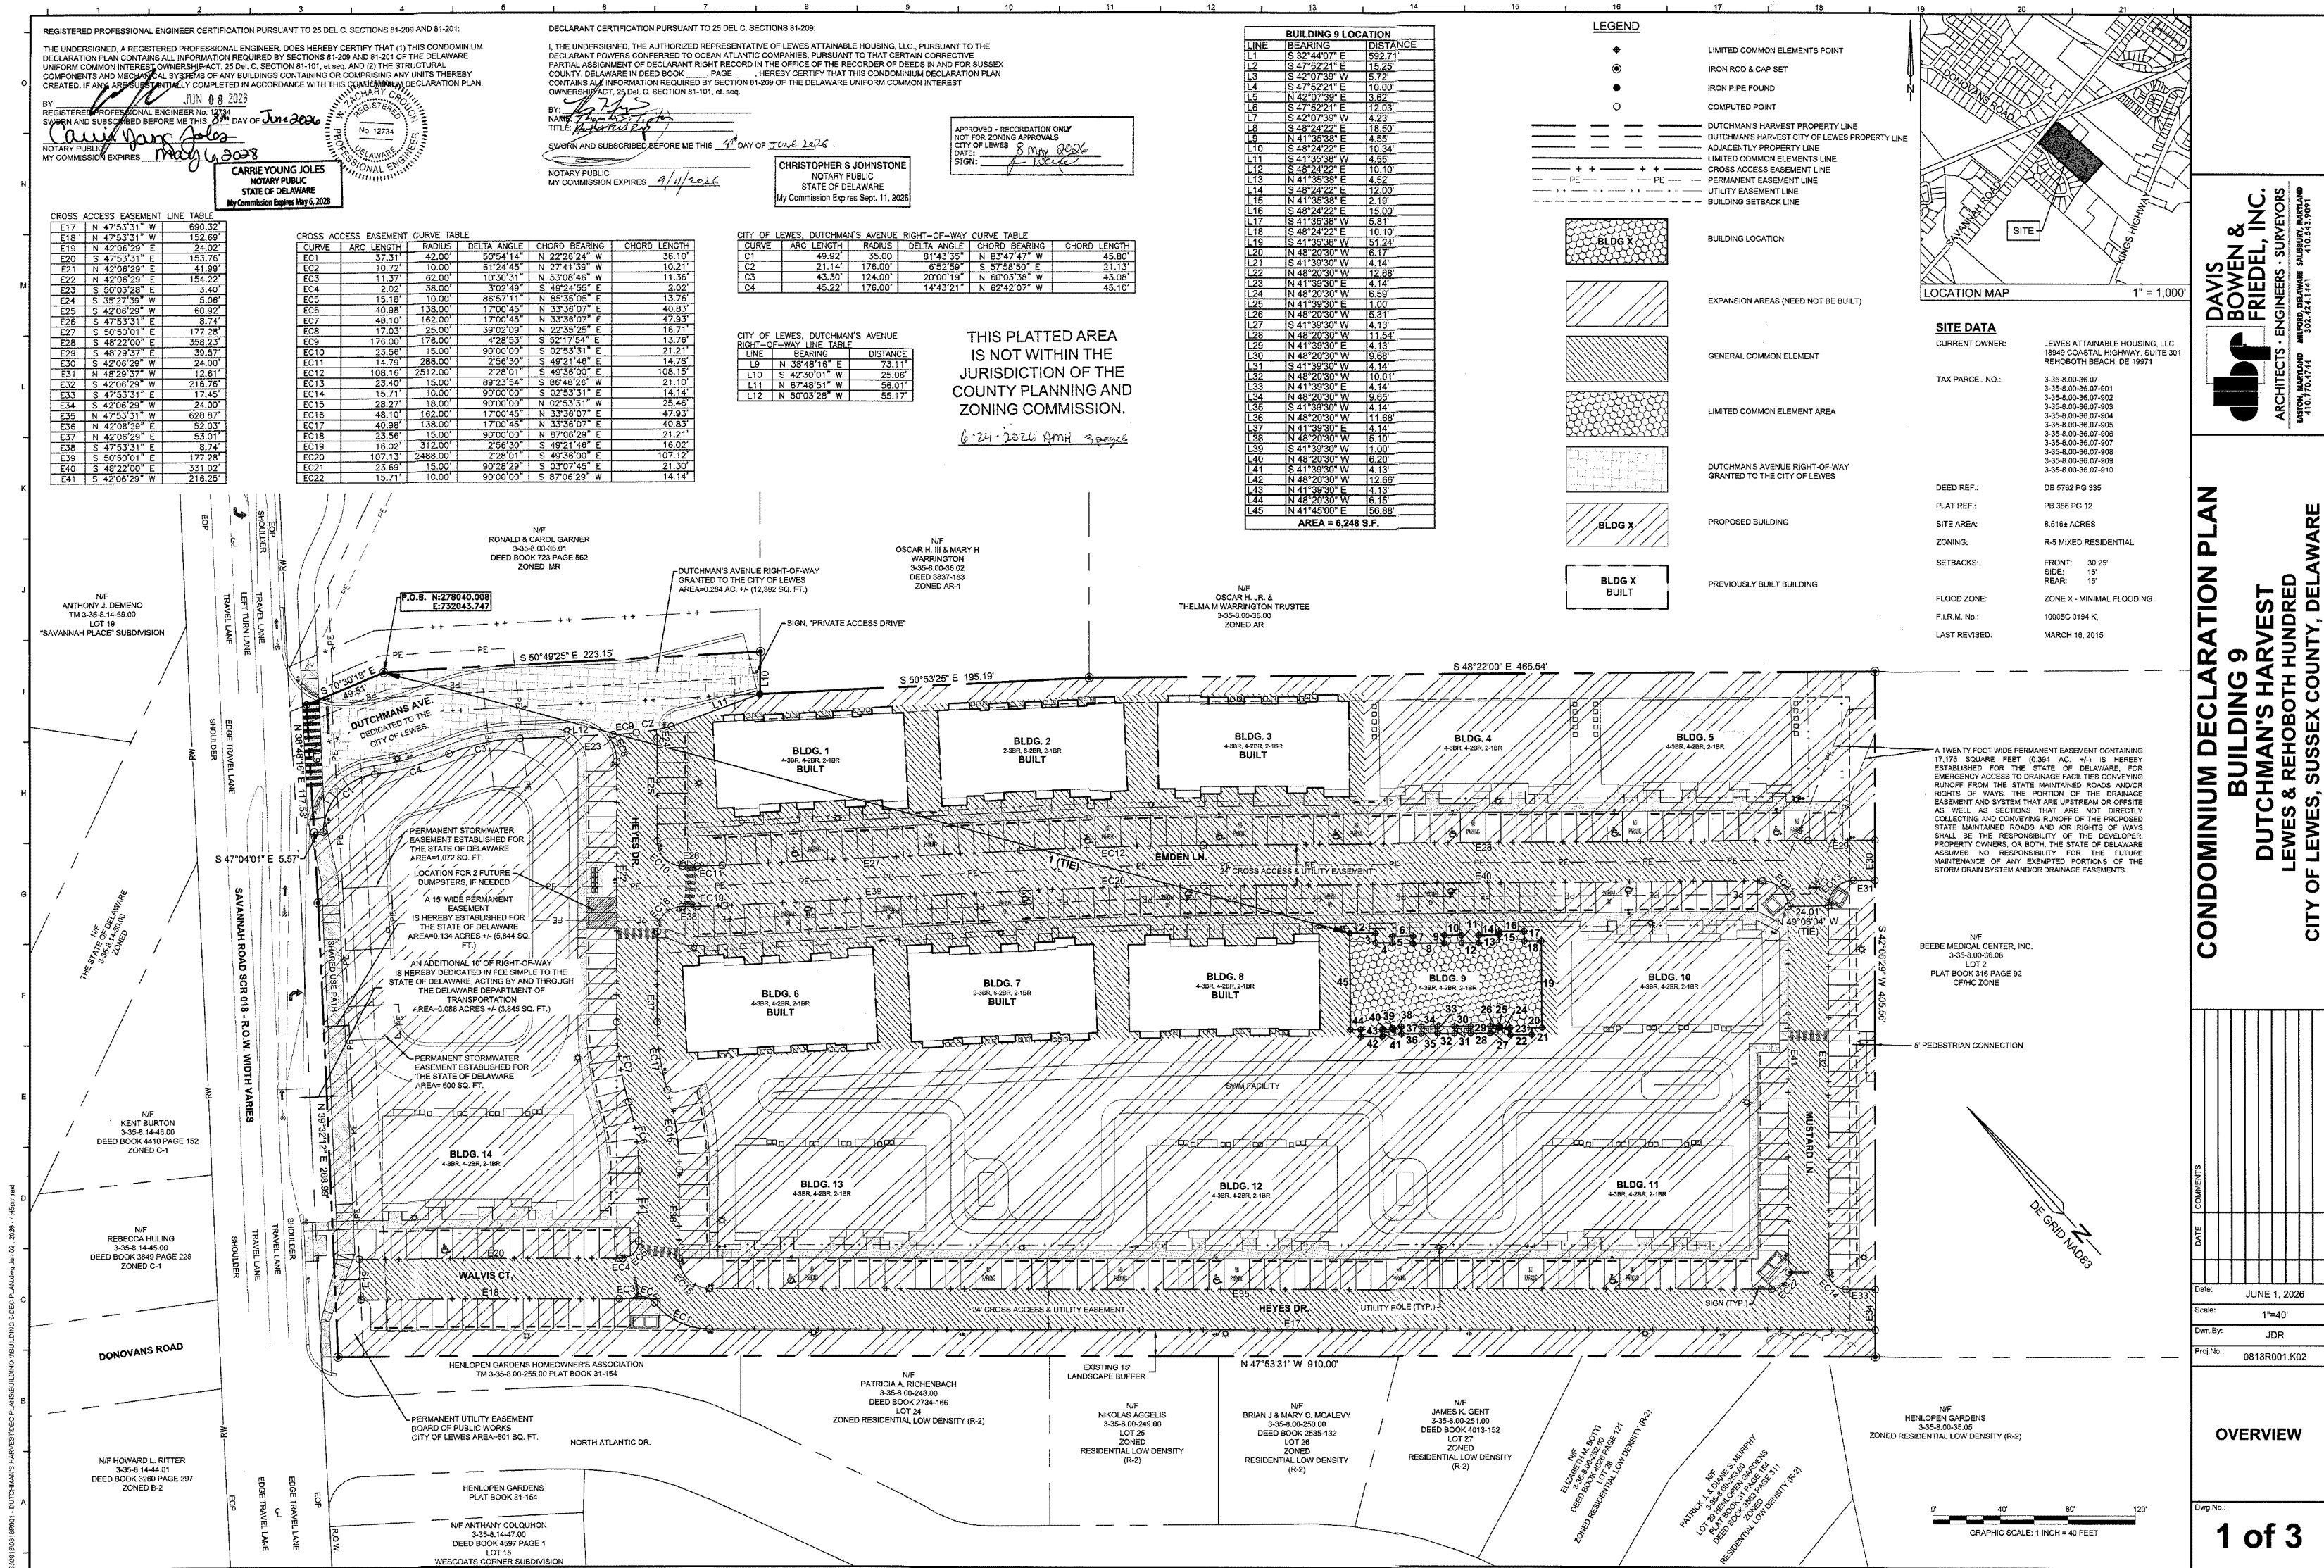


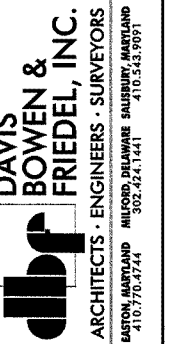

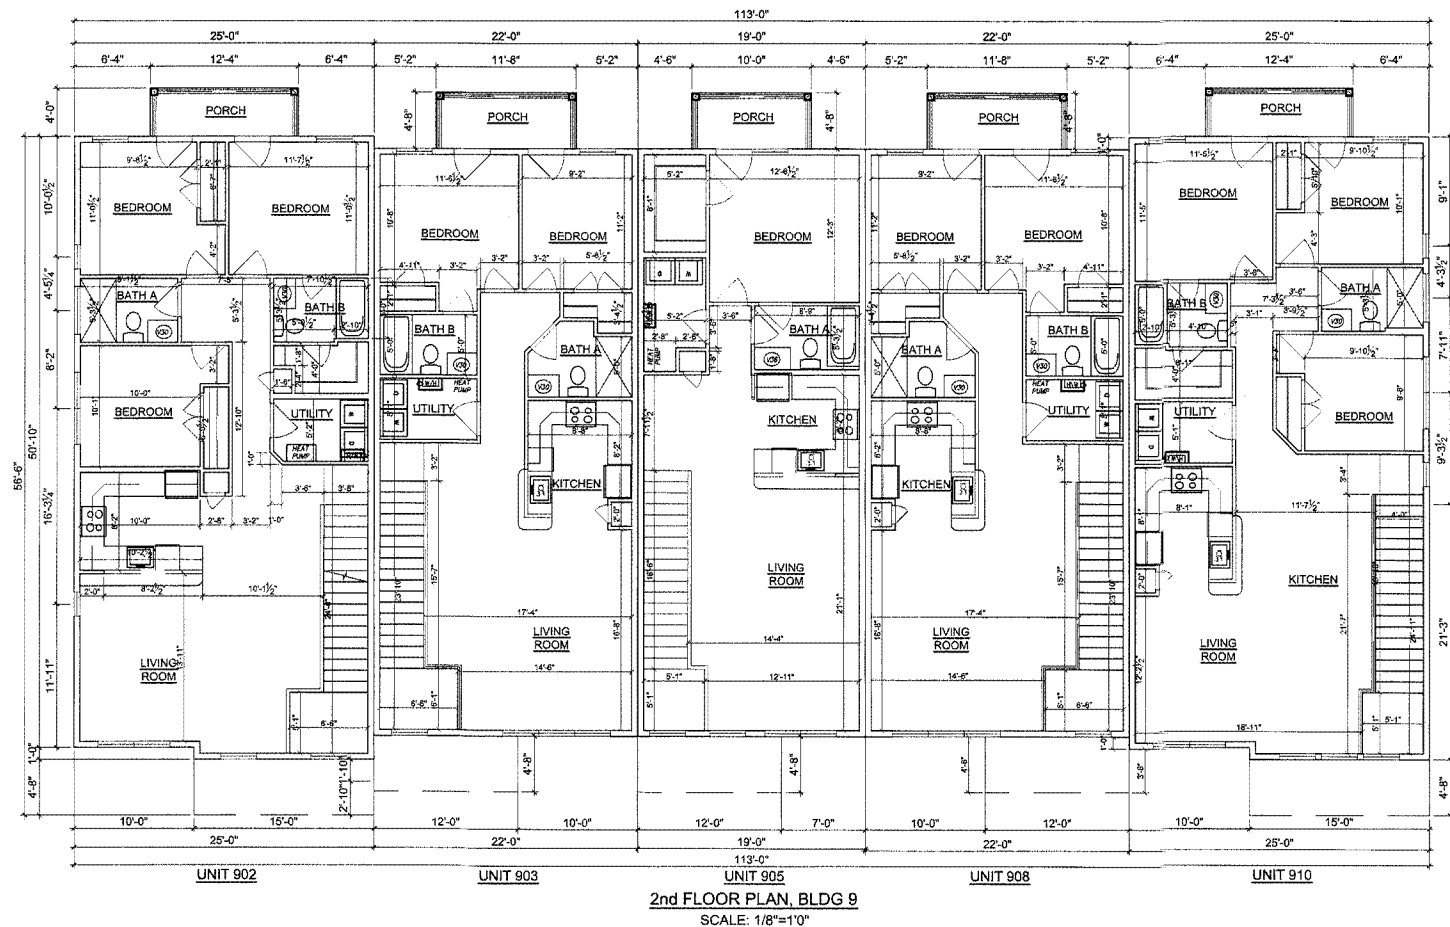

CONDOMINIUM DECLARATION PLAN
BUILDING 9
DUTCHMAN'S HARVEST
LEWES & REHOBOTH HUNDRED
CITY OF LEWES, SUSSEX COUNTY, DELAWARE


[illegible]

FLOOR PLANS


2 of 3



FRONT ELEVATION, BLDG 9
(4) 3 BEDROOM, (4) 2 BED (2) 1 BED
SCALE: 1/8"=1'0"

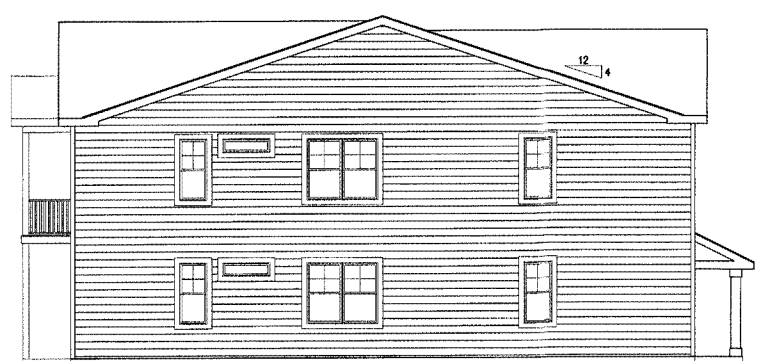

L. SIDE ELEVATION, BLDG 9
SCALE: 1/8"=1'0"

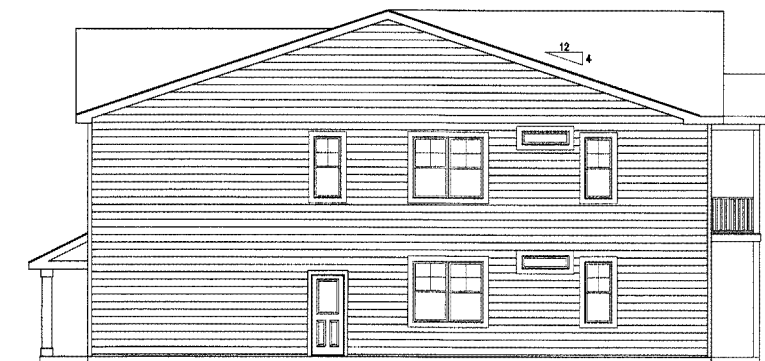

R. SIDE ELEVATION, BLDG 9
SCALE: 1/8"=1'0"




REAR ELEVATION W/ PORCHES, BLDG 9
SCALE: 1/8"=1'0"

LEGEND

⬤	LIMITED COMMON ELEMENTS POINT
●	IRON ROD & CAP SET
●	IRON PIPE FOUND
○	COMPUTED POINT

_____	DUTCHMAN'S HARVEST PROPERTY LINE
_____	DUTCHMAN'S HARVEST CITY OF LEWES PROPERTY LINE
_____	ADJACENTLY PROPERTY LINE
_____	LIMITED COMMON ELEMENTS LINE
_____ + + _____ + + _____	CROSS ACCESS EASEMENT LINE
_____ PE _____ PE _____	PERMANENT EASEMENT LINE
_____	UTILITY EASEMENT LINE
_____	BUILDING SETBACK LINE

BUILDING 9 LOCATION		
LINE	BEARING	DISTANCE
L1	S 32°44'07" E	592.71
L2	S 47°52'21" E	15.25
L3	S 42°07'39" W	5.72
L4	S 47°07'21" E	10.00
L5	S 12°02'39" W	12.03
L6	S 47°52'21" E	12.03
L7	S 42°07'39" W	4.23
L8	S 48°24'22" E	18.50
L9	S 48°24'22" E	18.50
L10	S 48°24'22" E	10.34
L11	N 11°35'38" W	4.55
L12	S 48°24'22" E	10.10
L13	N 41°35'38" E	4.52
L14	S 48°24'22" E	1.10
L15	N 41°35'38" E	2.10
L16	S 48°24'22" E	15.00
L17	N 41°35'38" E	5.81
L18	S 48°24'22" E	4.61
L19	N 41°35'38" W	51.24
L20	N 48°20'30" W	6.17
L21	S 41°39'30" W	4.14
L22	N 48°20'30" W	12.68
L23	N 41°39'30" E	4.14
L24	N 48°20'30" W	6.59
L25	N 41°39'30" E	1.00
L26	N 48°20'30" W	5.31
L27	N 41°39'30" E	4.14
L28	N 48°20'30" W	11.54
L29	N 41°39'30" E	4.13
L30	N 48°20'30" W	9.68
L31	S 41°39'30" E	4.14
L32	S 48°20'30" W	10.11
L33	N 41°39'30" E	4.14
L34	N 48°20'30" W	9.65
L35	N 41°39'30" E	4.14
L36	S 48°20'30" W	11.58
L37	N 41°39'30" E	4.14
L38	N 48°20'30" W	5.10
L39	S 41°39'30" W	1.00
L40	N 48°20'30" W	6.20
L41	N 41°39'30" E	4.14
L42	N 48°20'30" W	12.66
L43	N 41°39'30" E	4.13
L44	N 48°20'30" W	6.15
L45	N 41°45'00" E	16.88

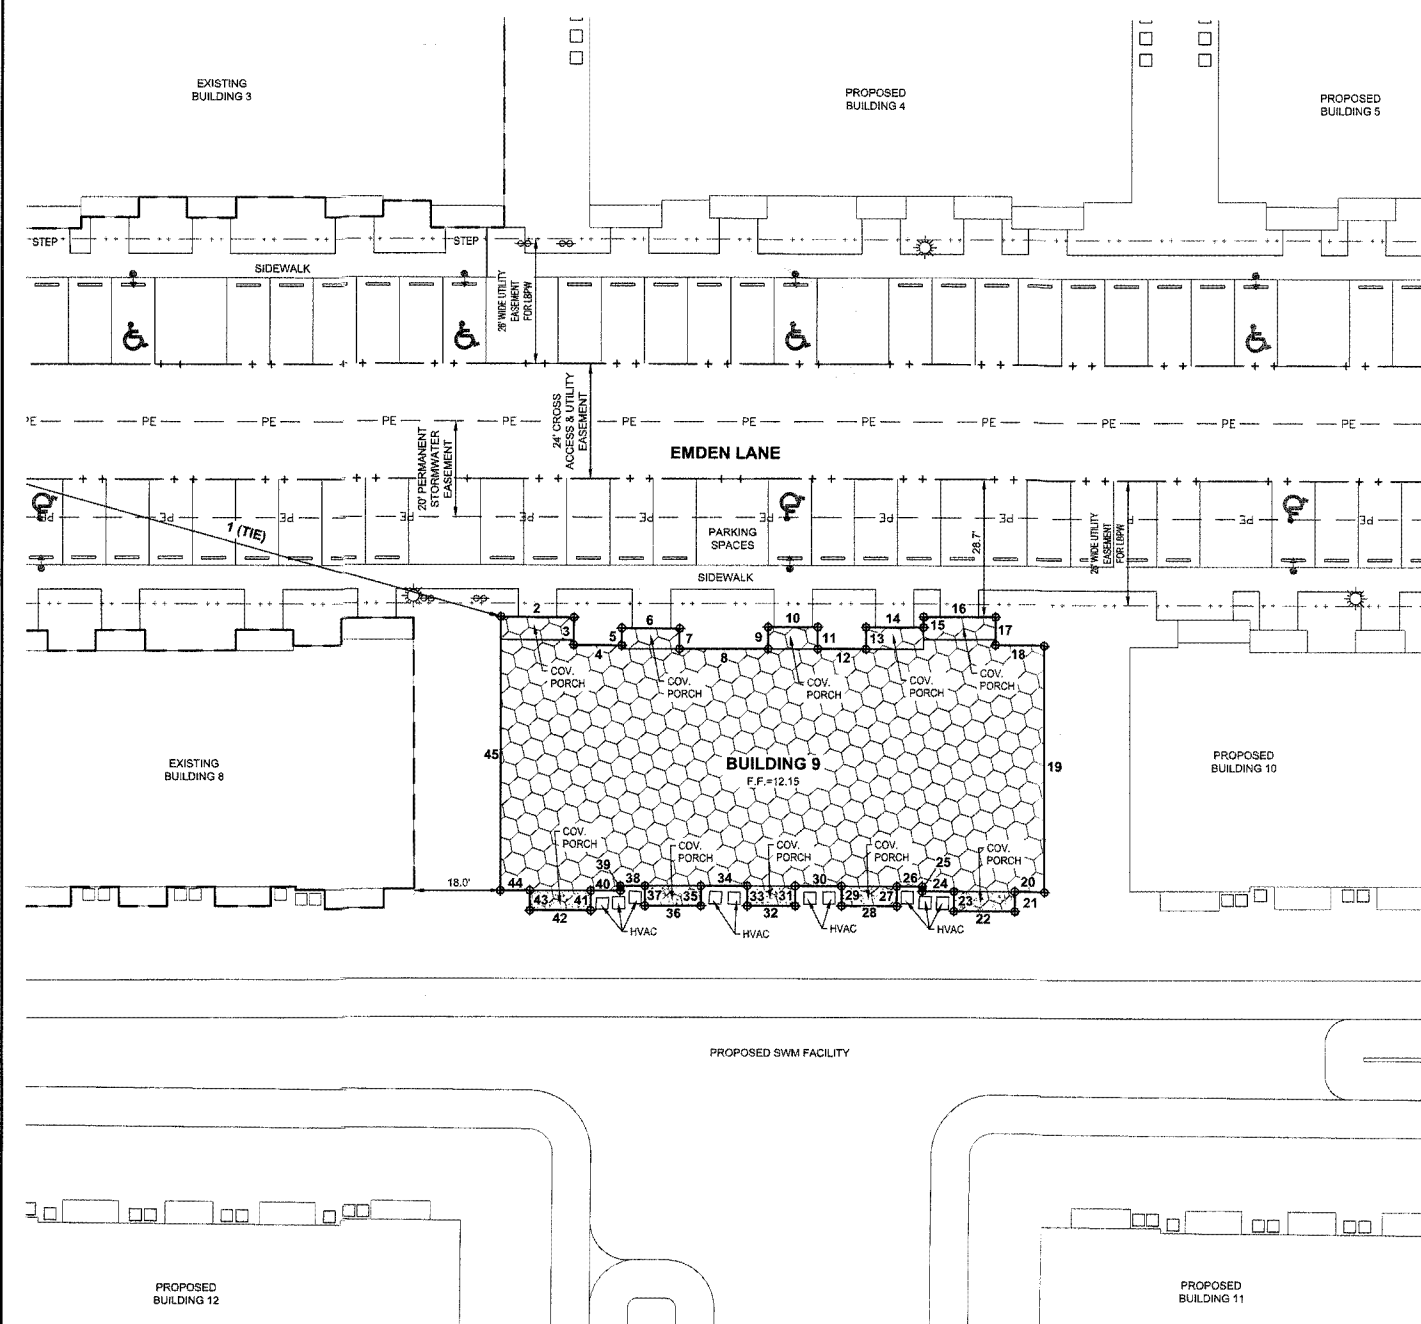

BUILDING 9 DETAIL
SCALE: 1"=20'